


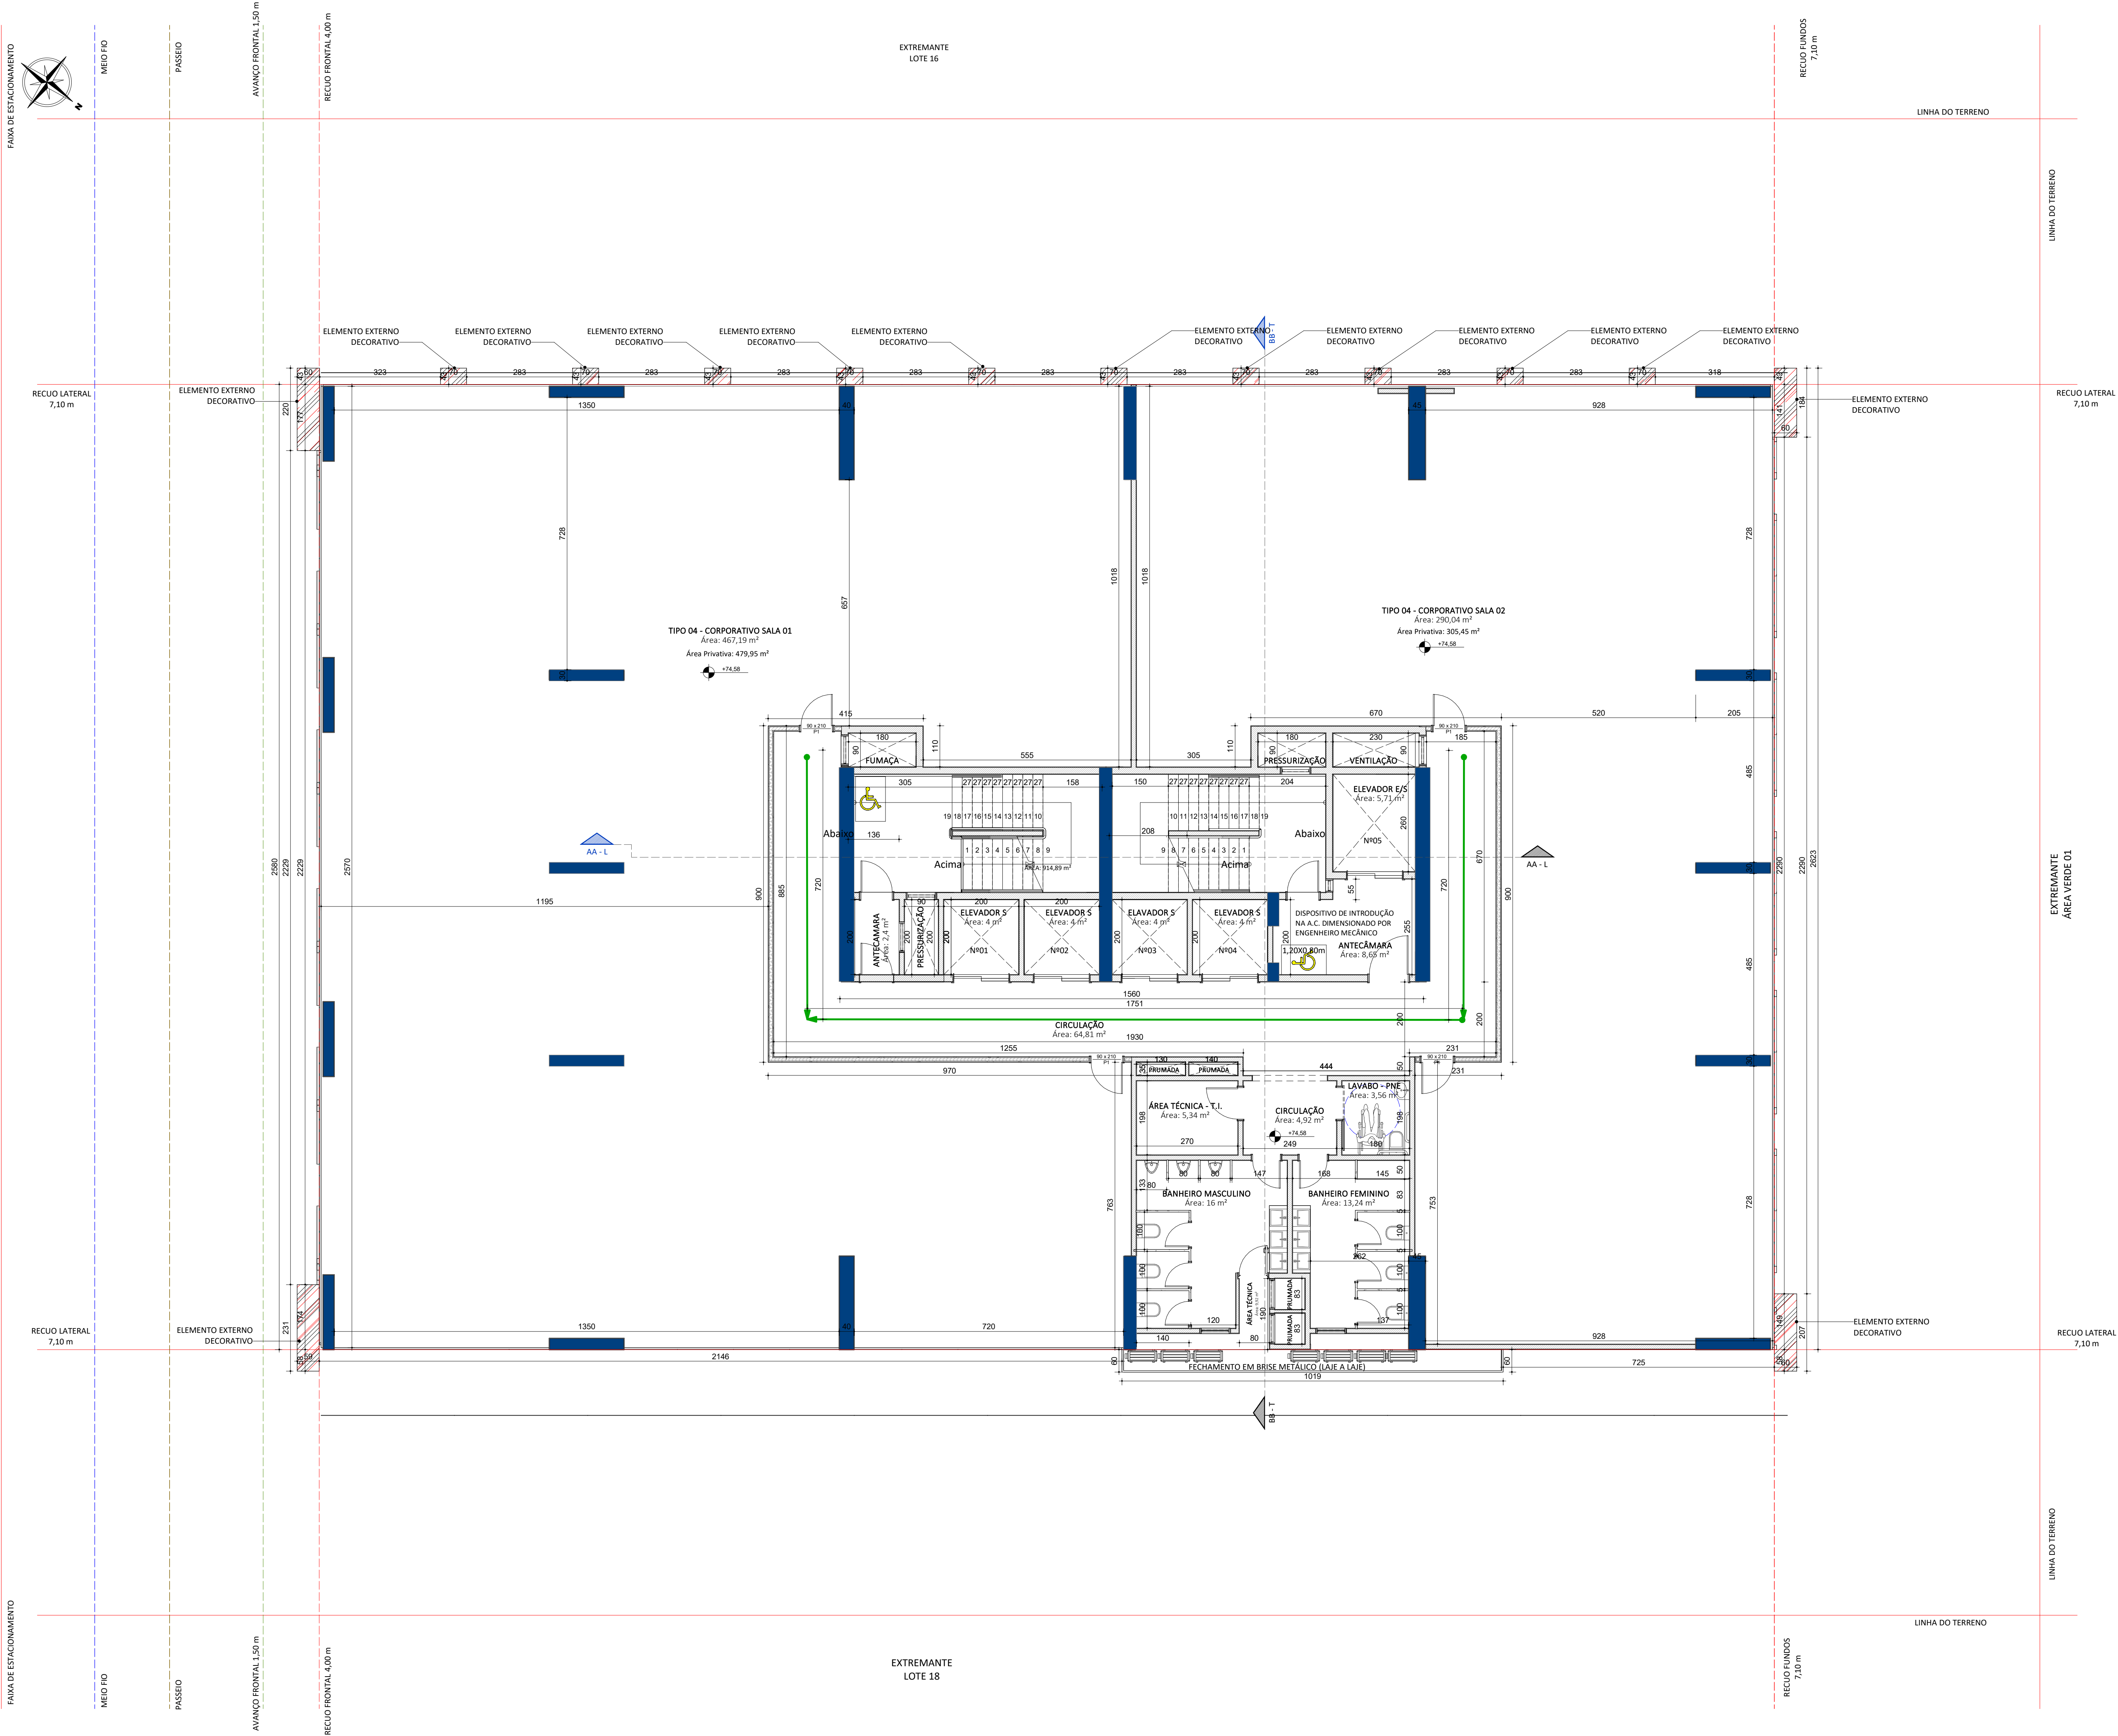

QUADRO DE JANELAS						
CÓD.	QT	COMPRIMENTO	ALTURA	PEITORIL	DESCRIÇÃO	ÁREA
J1	1	80	50	160	Esquadria de alumínio na cor branca / folha gold (Acos). Vidro acinzentado.	0,4 m²
J2	203	80	120	carretilha	VENEZIANA ANTECÂMARA	0,96 m²
J3	51	80	80	150	JANELA MAXIMA AR - 1 FOLHA - ALUMÍNIO E VIDRO	0,64 m²
J4	32	80	120	carretilha	VENEZIANA ANTECÂMARA - DIMENSIONADA ENG MEC	0,64 m²
J5	2	160	40	150	VENEZIANA VENTILADA	0,64 m²
J6	1	150	120	120	JANELA DE DESLIZAR - 2 FOLHAS - ALUMÍNIO E VIDRO	1,8 m²
J9	290					
J04	271	150	150	120	JANELA MAXIMA-AR - 1 FOLHA- ALU E VIDRO (ABERTURA 150x	2,25 m²

QUADRO DE PORTAS				
CÓD	QT	COMPRIMENTO	ALTURA	DESCRIÇÃO
A25	6	160	210	Porta Doble Interior de Gfro
P1	155	90	210	PORTA DE GIRO - 1 FOLHA - MADEIRA
P2	56	80	210	PORTA DE GIRO - 1 FOLHA - MADEIRA
P3	1	70	210	PORTA DE GIRO - 1 FOLHA - MADEIRA
P4	25	90	210	PORTA DE GIRO - 1 FOLHA - MADEIRA (PNE)
P5	6	90	210	PORTA DE GIRO - 1 FOLHA - VIDRO - SOB MEDIDA
P6	1	720	210	PORTA DE ABRIR - 1 FOLHA - MADEIRA (PNE)
P7	8	90	210	PORTA DE VIDRO - SOB MEDIDA
P8	2	300	300	PORTA AUTOMÁTICA - VIDRO TEMPERADO
P9	1	411	300	PORTA AUTOMÁTICA - VIDRO TEMPERADO
P9	150	70	180	PORTA DE GIRO - 1 FOLHA - SANTIFICADOS
P10	1	500	300	PORTÃO GARAGEM
P11	1	100	800	PORTA DE VIDRO - SOB MEDIDA
P11	1	383	300	PORTA DE VIDRO - SOB MEDIDA
PC01	1	300	210	PORTA 1 FOLHA - ALUMÍNIO COM BARRA ANTI-PANICO
PC1 01	94	90	210	PORTA DE GIRO - 1 FOLHA - CORTA FOGO
PC1 02	31	110	210	PORTA DE GIRO - 1 FOLHA - CORTA FOGO
PS	158	150	210	PORTA DO ELEVADOR
PD01	1	350	300	PORTÃO GARAGEM
VN2 1	6	130	210	PORTA VENEZIANA
VN2 2	35	75	210	PORTA VENEZIANA
VN2 3	2	89	120	PORTA VENEZIANA - VISTA
	742			

REVISÃO	ASSUNTO	DESENHO	RESPONSÁVEL	DATA
R1	1º ANÁLISE	GIOVANNI D.	RS CONCEPT	11/11/2024

RS
CONCEPT

PROJETO

OBRA

RESP. TÉCNICO

PROPRIETÁRIO

DATA
17/05/2024

OBRA TIPO
EDIFÍCIO COMERCIAL E RESIDENCIAL MULTIFAMILIAR

PROTÓCOLO RS
70.2021 LK9

CONTEÚDO
PLANTA DO 24º PAVIMENTO - TIPO 04
QUADRO DE ESQUADRIAS

OBSERVAÇÕES IMPORTANTES:
Declaram que a aprovação do projeto não implica no reconhecimento por parte da Prefeitura de
Belo Horizonte do conteúdo do projeto.
Declaram que as informações e os cálculos das áreas contidas nesse projeto, são verdadeiras e de
sua responsabilidade de acordo com a lei.
Declaram, como autor do projeto, que estão cientes e que assumem a responsabilidade de qualquer alteração
na forma executada de edificação, sob pena de aplicação das sanções previstas no art. 1º da Lei nº 12.332/2010.

ESCALA
INDICADA

ARQUITETÔNICO

LOTUS BUSINESS CENTER
RUA PROJETADA (AVENIDA RIO PEREQUE), Nº 539 - LOTE Nº 16 E LOTE Nº 17
LOTEAMENTO ANDORINHA CENTER, PORTO BELO SC

HECTOR RHAVI DA COSTA
CAU: A190987-8

L K NOVE EMPREENDIMENTOS IMOBILIÁRIOS SPE LTDA
CNPJ 44.023.808/1001-60

DATA
17/05/2024

OBRA TIPO
EDIFÍCIO COMERCIAL E RESIDENCIAL MULTIFAMILIAR

PROTÓCOLO RS
70.2021 LK9

CONTEÚDO
PLANTA DO 24º PAVIMENTO - TIPO 04
QUADRO DE ESQUADRIAS

OBSERVAÇÕES IMPORTANTES:
Declaram que a aprovação do projeto não implica no reconhecimento por parte da Prefeitura de
Belo Horizonte do conteúdo do projeto.
Declaram que as informações e os cálculos das áreas contidas nesse projeto, são verdadeiras e de
sua responsabilidade de acordo com a lei.
Declaram, como autor do projeto, que estão cientes e que assumem a responsabilidade de qualquer alteração
na forma executada de edificação, sob pena de aplicação das sanções previstas no art. 1º da Lei nº 12.332/2010.

ESCALA
INDICADA

PRANCHIA

11
/ 21

Rua 292, nº3.201 | sala 01 | Itapema/SC

Fone: (47) 3368 8110