


CANTERO CENTRAL DA AVENIDA

RUA PROJETADA  
AVENIDÃO PEREQUÊ

CANTERO CENTRAL DA AVENIDA

RESERVATÓRIO  
ESCALA 1:75

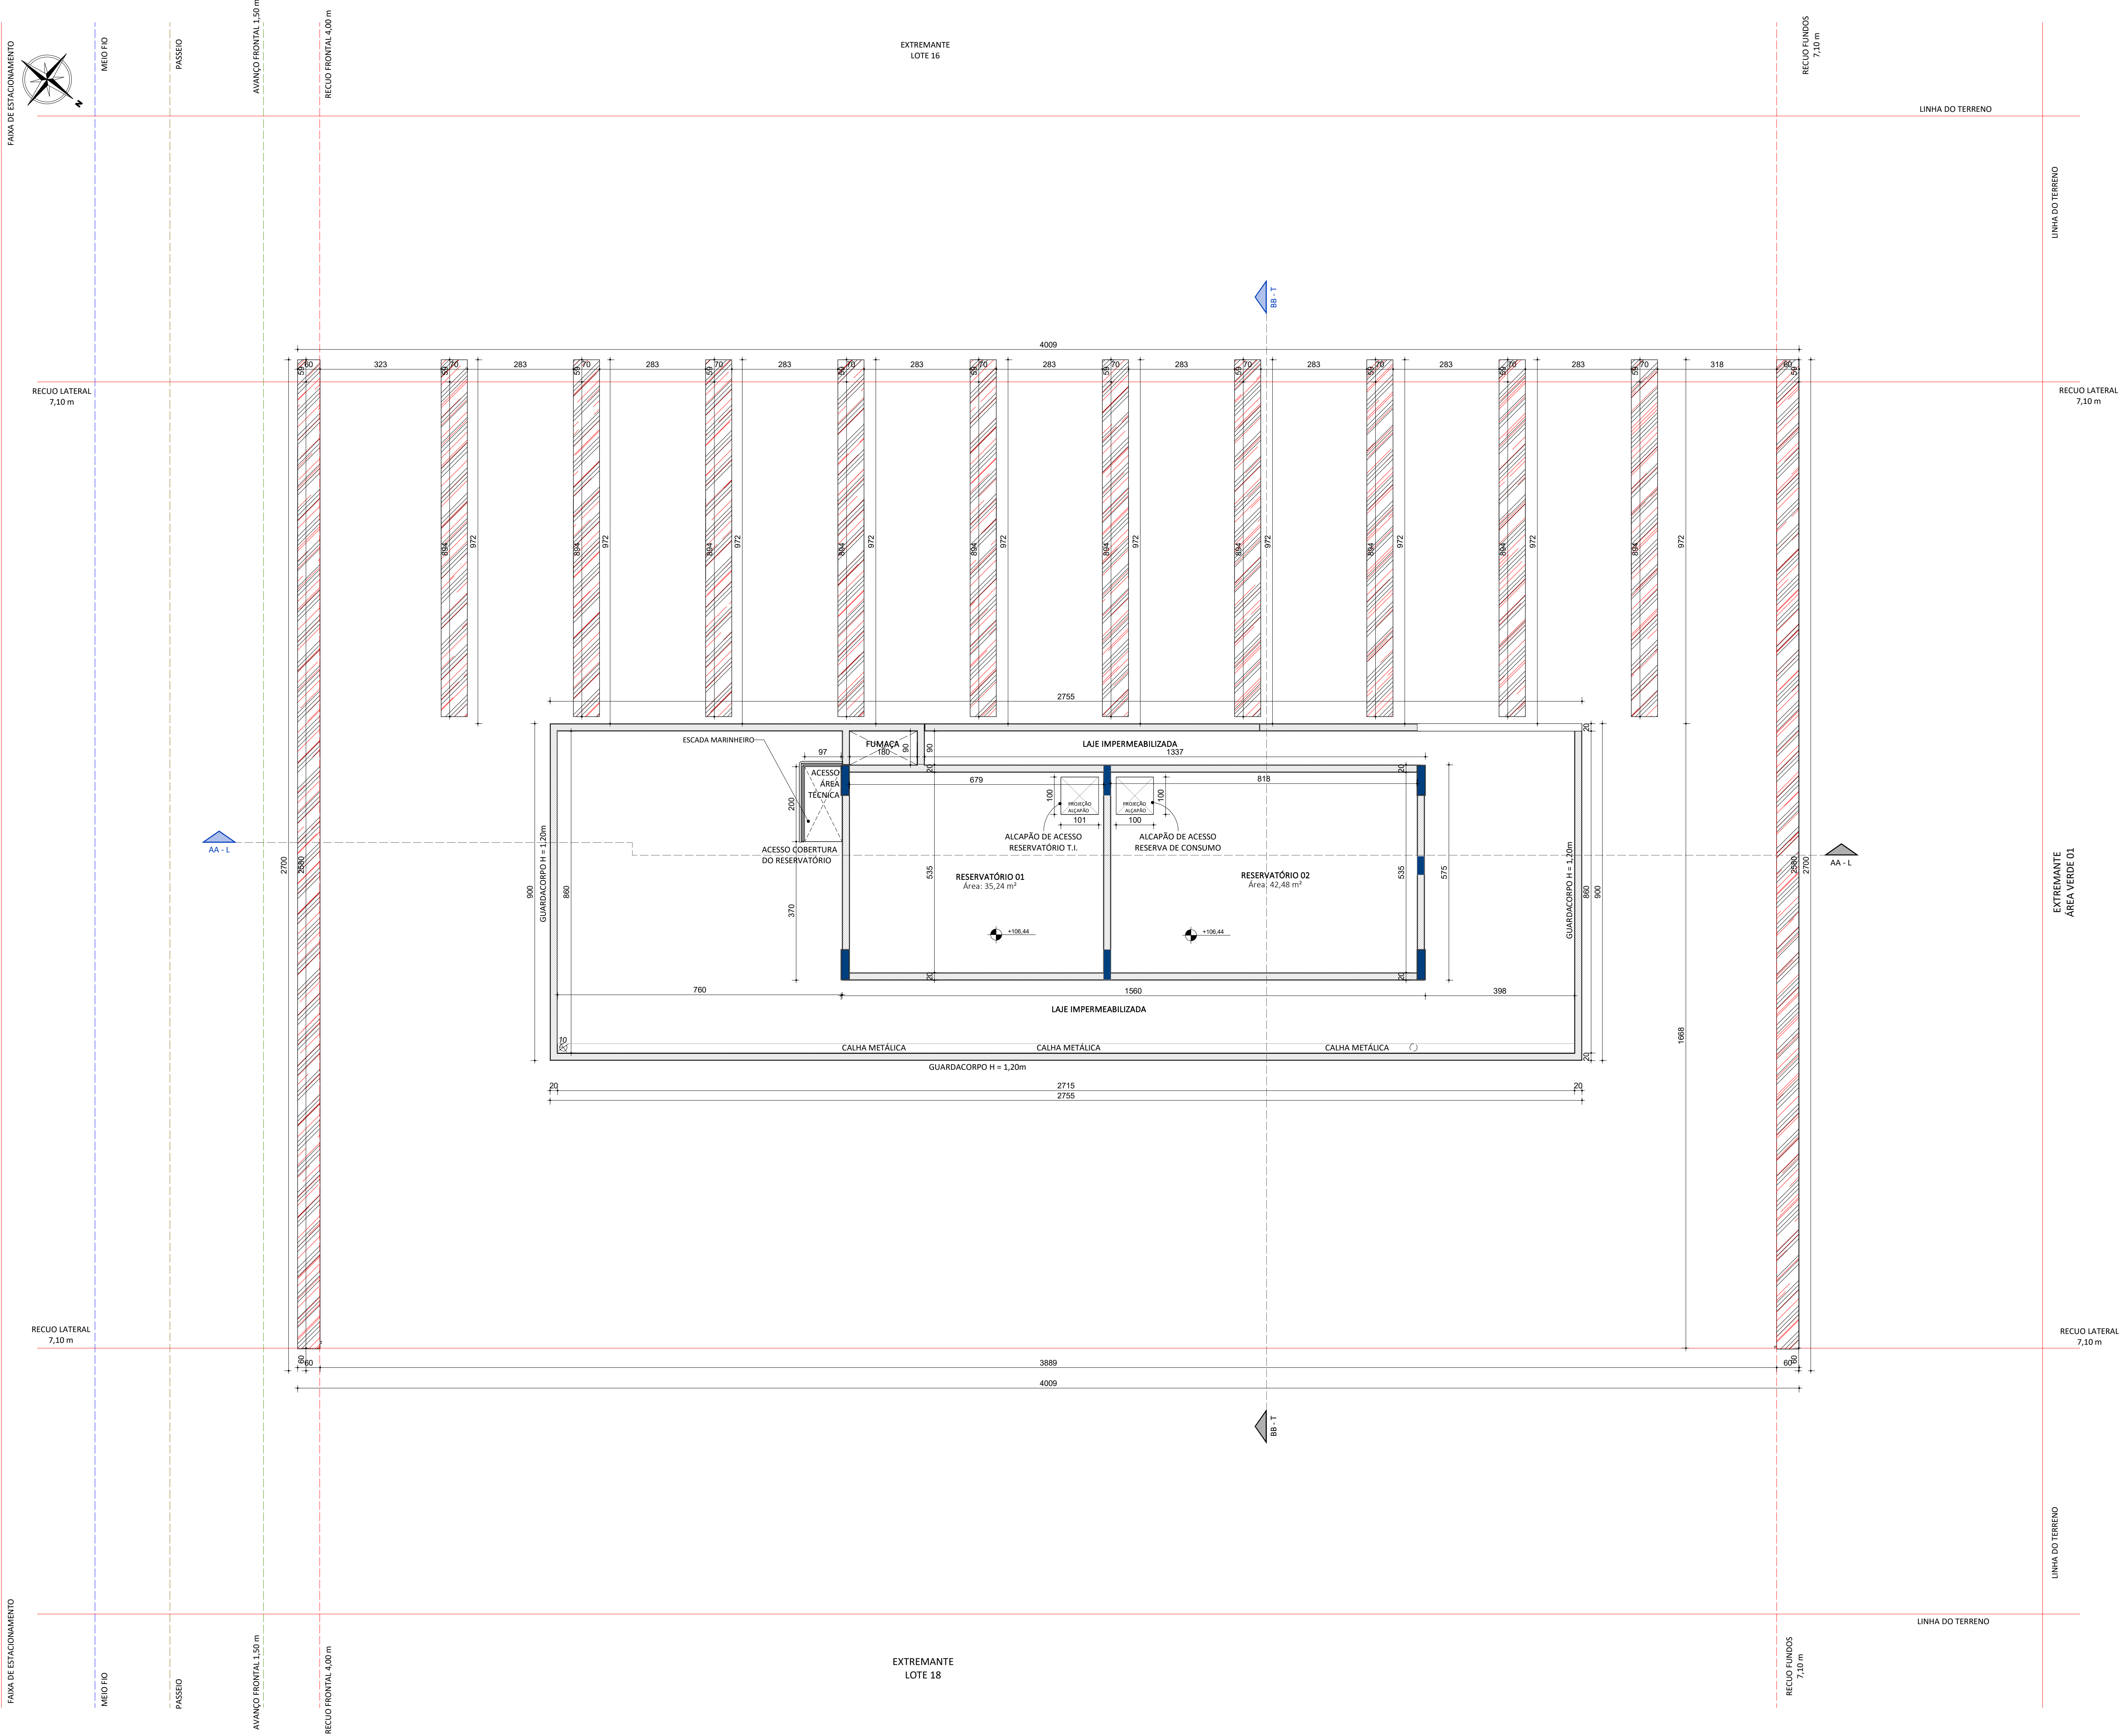

| QUADRO DE JANELAS |     |             |        |            |                                                                          |         |
|-------------------|-----|-------------|--------|------------|--------------------------------------------------------------------------|---------|
| CÓD.              | QT  | COMPRIMENTO | ALTURA | PEITORIL   | DESCRIÇÃO                                                                | ÁREA    |
| J1                | 1   | 80          | 150    | 160        | Esquadria de alumínio na cor branca / vidro gold (Acoss). Vidro acústico | 0,6 m²  |
| J2                | 203 | 80          | 120    | carretilha | VENEZIANA ANTECÂMARA                                                     | 0,96 m² |
| J3                | 51  | 80          | 80     | 150        | JANELA MAXIMA-AR - 1 FOLHA - ALUMÍNIO E VIDRO                            | 0,64 m² |
| J4                | 32  | 80          | 120    | carretilha | VENEZIANA ANTECÂMARA - DIMENSIONADA ENG MEC                              | 0,64 m² |
| J5                | 2   | 160         | 40     | 170        | VENEZIANA VENTILADA                                                      | 0,64 m² |
| J6                | 1   | 150         | 120    | 120        | JANELA DE DESLIZAR - 2 FOLHAS - ALUMÍNIO E VIDRO                         | 1,8 m²  |
| J95               |     |             |        |            |                                                                          |         |
| J04               | 271 | 150         | 150    | 120        | JANELA MAXIM-AR - 1 FOLHA - ALU E VIDRO (ABERTURA 150)                   | 2,25 m² |

| QUADRO DE PORTAS |     |             |        |                                               |
|------------------|-----|-------------|--------|-----------------------------------------------|
| CÓD              | QT  | COMPRIMENTO | ALTURA | DESCRIÇÃO                                     |
| A25              | 6   | 160         | 210    | Porta Dupla Interior de Giro                  |
| P1               | 155 | 90          | 210    | PORTA DE GIRO - 1 FOLHA - MADEIRA             |
| P2               | 56  | 80          | 210    | PORTA DE GIRO - 1 FOLHA - MADEIRA             |
| P3               | 1   | 70          | 210    | PORTA DE GIRO - 1 FOLHA - MADEIRA             |
| P4               | 25  | 90          | 210    | PORTA DE DESLIZAR - 1 FOLHA - MADEIRA (PNE)   |
| P5               | 6   | 90          | 210    | PORTA DE GIRO - 1 FOLHA - VIDRO - SOB MEDIDA  |
| P6               | 1   | 720         | 210    | PORTA DE ABRIR - 1 FOLHA - MADEIRA (PNE)      |
| P7               | 8   | 90          | 210    | PORTA AUTOMÁTICA - VIDRO TEMPERADO            |
| P8               | 2   | 300         | 300    | PORTA AUTOMÁTICA - VIDRO TEMPERADO            |
| P9               | 11  | 451         | 300    | PORTA DE GIRO - 1 FOLHA - SANITÁRIOS          |
| P10              | 1   | 500         | 300    | PORTÃO GARAGEM                                |
| P11              | 1   | 100         | 300    | PORTA DE VIDRO - SOB MEDIDA                   |
| P12              | 1   | 383         | 300    | PORTA DE VIDRO - SOB MEDIDA                   |
| P13              | 1   | 200         | 210    | PORTA 1 FOLHA - ALÇOFÃO COM ANTRA ANTI-PANICO |
| P14              | 94  | 90          | 210    | PORTA DE GIRO - 1 FOLHA - CORTA FOGO          |
| P15              | 31  | 110         | 210    | PORTA DE GIRO - 1 FOLHA - CORTA FOGO          |
| P16              | 158 | 150         | 210    | PORTA DO ELEVADOR                             |
| P17              | 1   | 350         | 300    | PORTÃO GARAGEM                                |
| P18              | 5   | 130         | 210    | PORTA VENEZIANA                               |
| P19              | 35  | 75          | 210    | PORTA VENEZIANA                               |
| P20              | 2   | 80          | 120    | PORTA VENEZIANA - VISTA                       |
| P21              | 742 |             |        |                                               |

| REVISÃO | ASSUNTO    | DESENHO     | RESPONSÁVEL | DATA       |
|---------|------------|-------------|-------------|------------|
| R1      | 1º ANÁLISE | GIOVANNI D. | RS CONCEPT  | 11/11/2024 |

# ARQUITETÔNICO

**LOTUS BUSINESS CENTER**  
RUA PROJETADA (AVENIDA RIO PEREQUÊ), Nº 539 - LOTE Nº 16 E LOTE Nº 17  
LOTEAMENTO ANDORINHA CENTER, PORTO BELO SC

PROJETO

OBRA

RESP. TÉCNICO

PROPRIETÁRIO

DATA  
17/05/2024

OBRA TIPO  
EDIFÍCIO COMERCIAL E RESIDENCIAL MULTIFAMILIAR

PROTÓCOLO RS  
70.2021 LK9

CONTEÚDO  
PLANTA RESERVATÓRIO  
QUADRO DE ESQUADRIAS

OBSERVAÇÕES IMPORTANTES:  
Declaram que a aprovação do projeto não implica no reconhecimento por parte da Prefeitura do Brasil do empreendimento de loteamento.  
Declaram que as informações e os cálculos das áreas contidas nesse projeto, são verdadeiras e de sua responsabilidade de acordo com a lei.  
Declaram, como autor do projeto, que estão cientes de que ficam obrigados ao cumprimento das normas técnicas de engenharia aplicáveis - ABNT NBR 16203.

ESCALA  
INDICADA

PRANCHIA

16 / 21