


CANTERO CENTRAL DA AVENIDA

RUA PROJETADA
AVENIDA RIO PEREQUE

CANTERO CENTRAL DA AVENIDA

3º PAVTO - GARAGEM G2
ESCALA 1 : 75

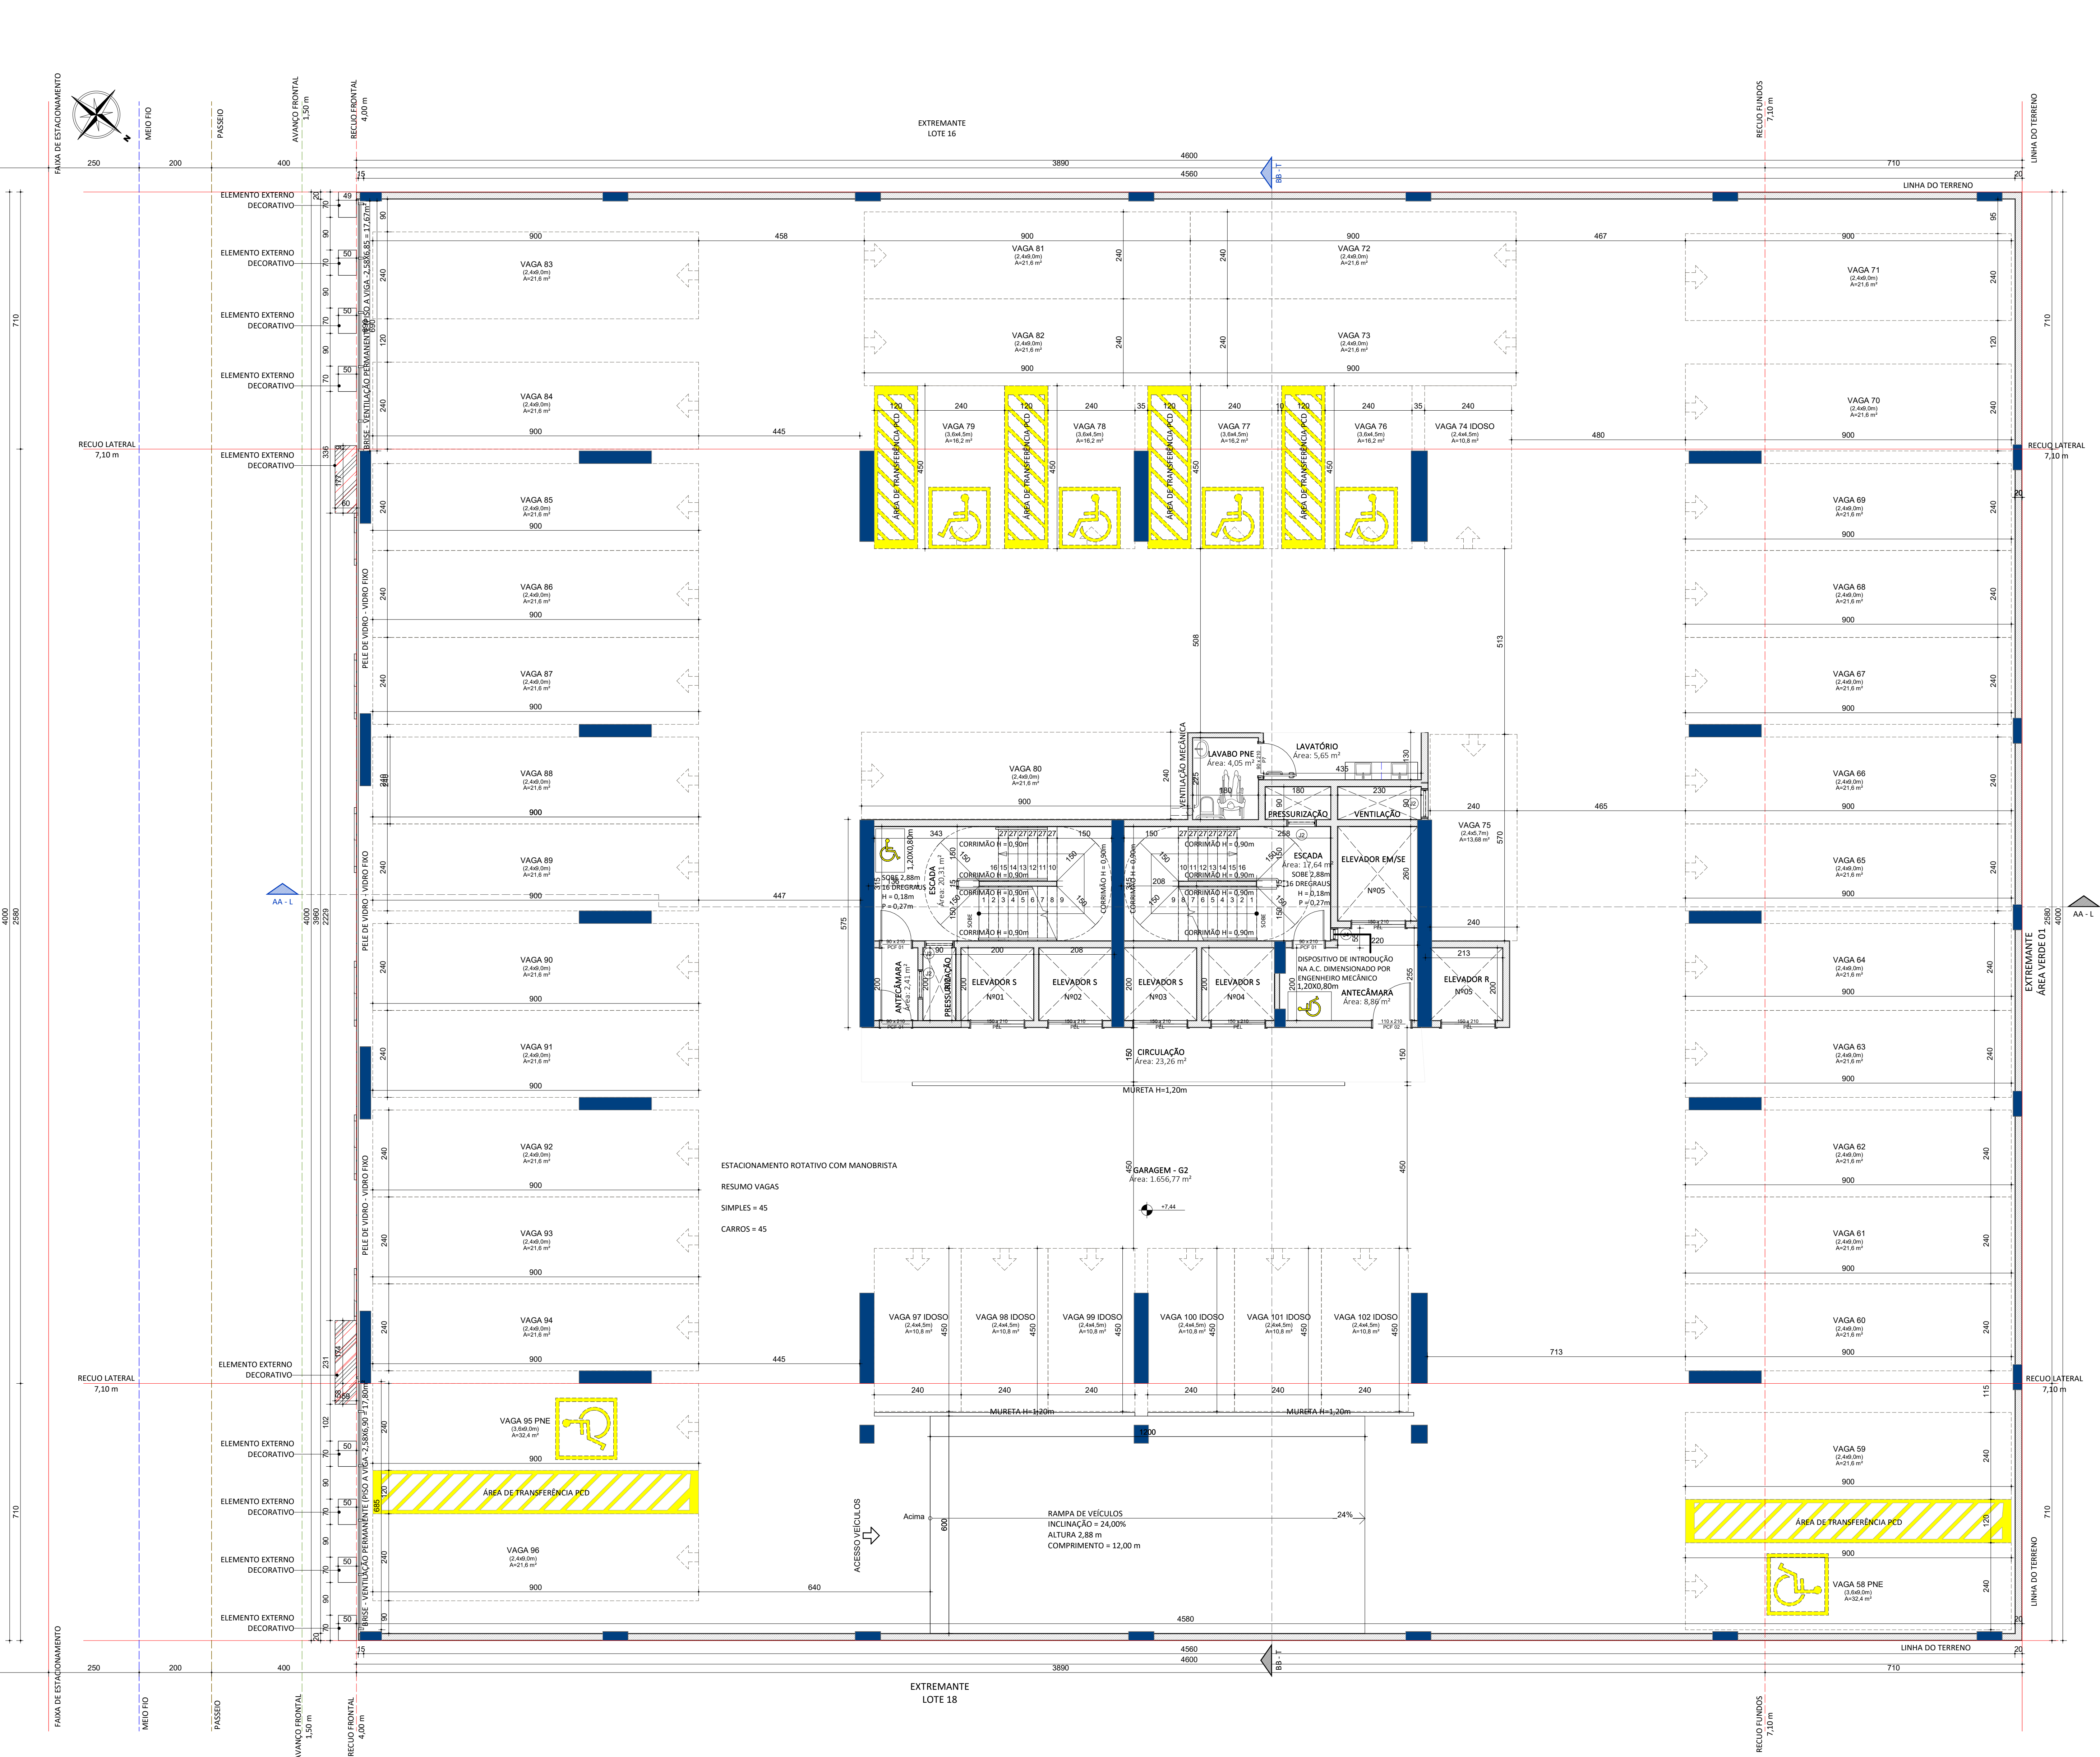

QUADRO DE JANELAS						
CÓD.	QT	COMPRIMENTO	ALTURA	PEITORIL	DESCRIÇÃO	ÁREA
J1	1	80	150	160	Esquadria de alumínio na cor branca / folha gold (Acco). Vitrô acobido	0,6 m²
J2	203	80	120	«verreco»	VENEZIANA ANTECÂMARA	0,96 m²
J3	51	80	80	150	JANELA MAXIM-AR - 1 FOLHA - ALUMÍNIO E VIDRO	0,64 m²
J4	32	80	120	«verreco»	VENEZIANA ANTECÂMARA - DIMENSIONADA ENG MEC	0,64 m²
J5	2	160	40	150	VENEZIANA VENTILADA	0,64 m²
J6	1	150	120	120	JANELA DE DESLIZAR - 2 FOLHAS - ALUMÍNIO E VIDRO	1,8 m²
J04	271	150	150	120	JANELA MAXIM-AR - 1 FOLHA - ALU E VIDRO (ABERTURA 15º)	2,25 m²

QUADRO DE VAGAS		
NÍVEL	QTDE	
PAV. 01 - TERREO	15	
PAV. 3 - GARAGEM G3	45	
PAV. 5 - GARAGEM G5	45	
PAV. 4 - GARAGEM G4	46	
PAV. 6 - GARAGEM G6	46	
	243	

REVISÃO	ASSUNTO	DESENHO	RESPONSÁVEL	DATA
R1	1º ANÁLISE	GIOVANNI D.	RS CONCEPT	11/11/2024



PROJETO
ARQUITETÔNICO
OBRA
LOTUS BUSINESS CENTER
RUA PROJETADA (AVENIDA RIO PEREQUE), Nº 539 - LOTE Nº 16 E LOTE Nº 17
LOTEAMENTO ANDORINHA CENTER, PORTO BELO SC

RESP. TÉCNICO HÉCTOR RHAVI DA COSTA CAU: A190987-8	PROPRIETÁRIO L K NOVE EMPREENDIMENTOS IMOBILIÁRIOS SPE LTDA CNPJ 44.023.808/1001-60
--	---

DATA 17/05/2024	OBRA TIPO EDIFÍCIO COMERCIAL E RESIDENCIAL MULTIFAMILIAR
PROTOCOLO RS 70.2021.193	CONTEÚDO PLANTA DO 3º PAVIMENTO GARAGEM - G2 QUADRO DE ESQUADRIAS

OBSERVAÇÕES IMPORTANTES:
1. Declaram que a aprovação do projeto não implica no reconhecimento por parte da Prefeitura de Minas Gerais do projeto de obra.
2. Declaram que as informações e os cálculos das áreas contidas nesse projeto, são verdadeiras e de sua responsabilidade de acordo com o teor.
3. Declaram, como autor do projeto, que estão cientes que não foram atendidas as exigências contantes na norma brasileira de edificações habitação - ABNT NBR 15303.

ESCALA
INDICADA