


CANTIERO CENTRAL DA AVENIDA

RUA PROJETADA
AVENIDÁRIO PEREQUE

CANTIERO CENTRAL DA AVENIDA

4º PAVTO - GARAGEM G3
ESCALA 1:75

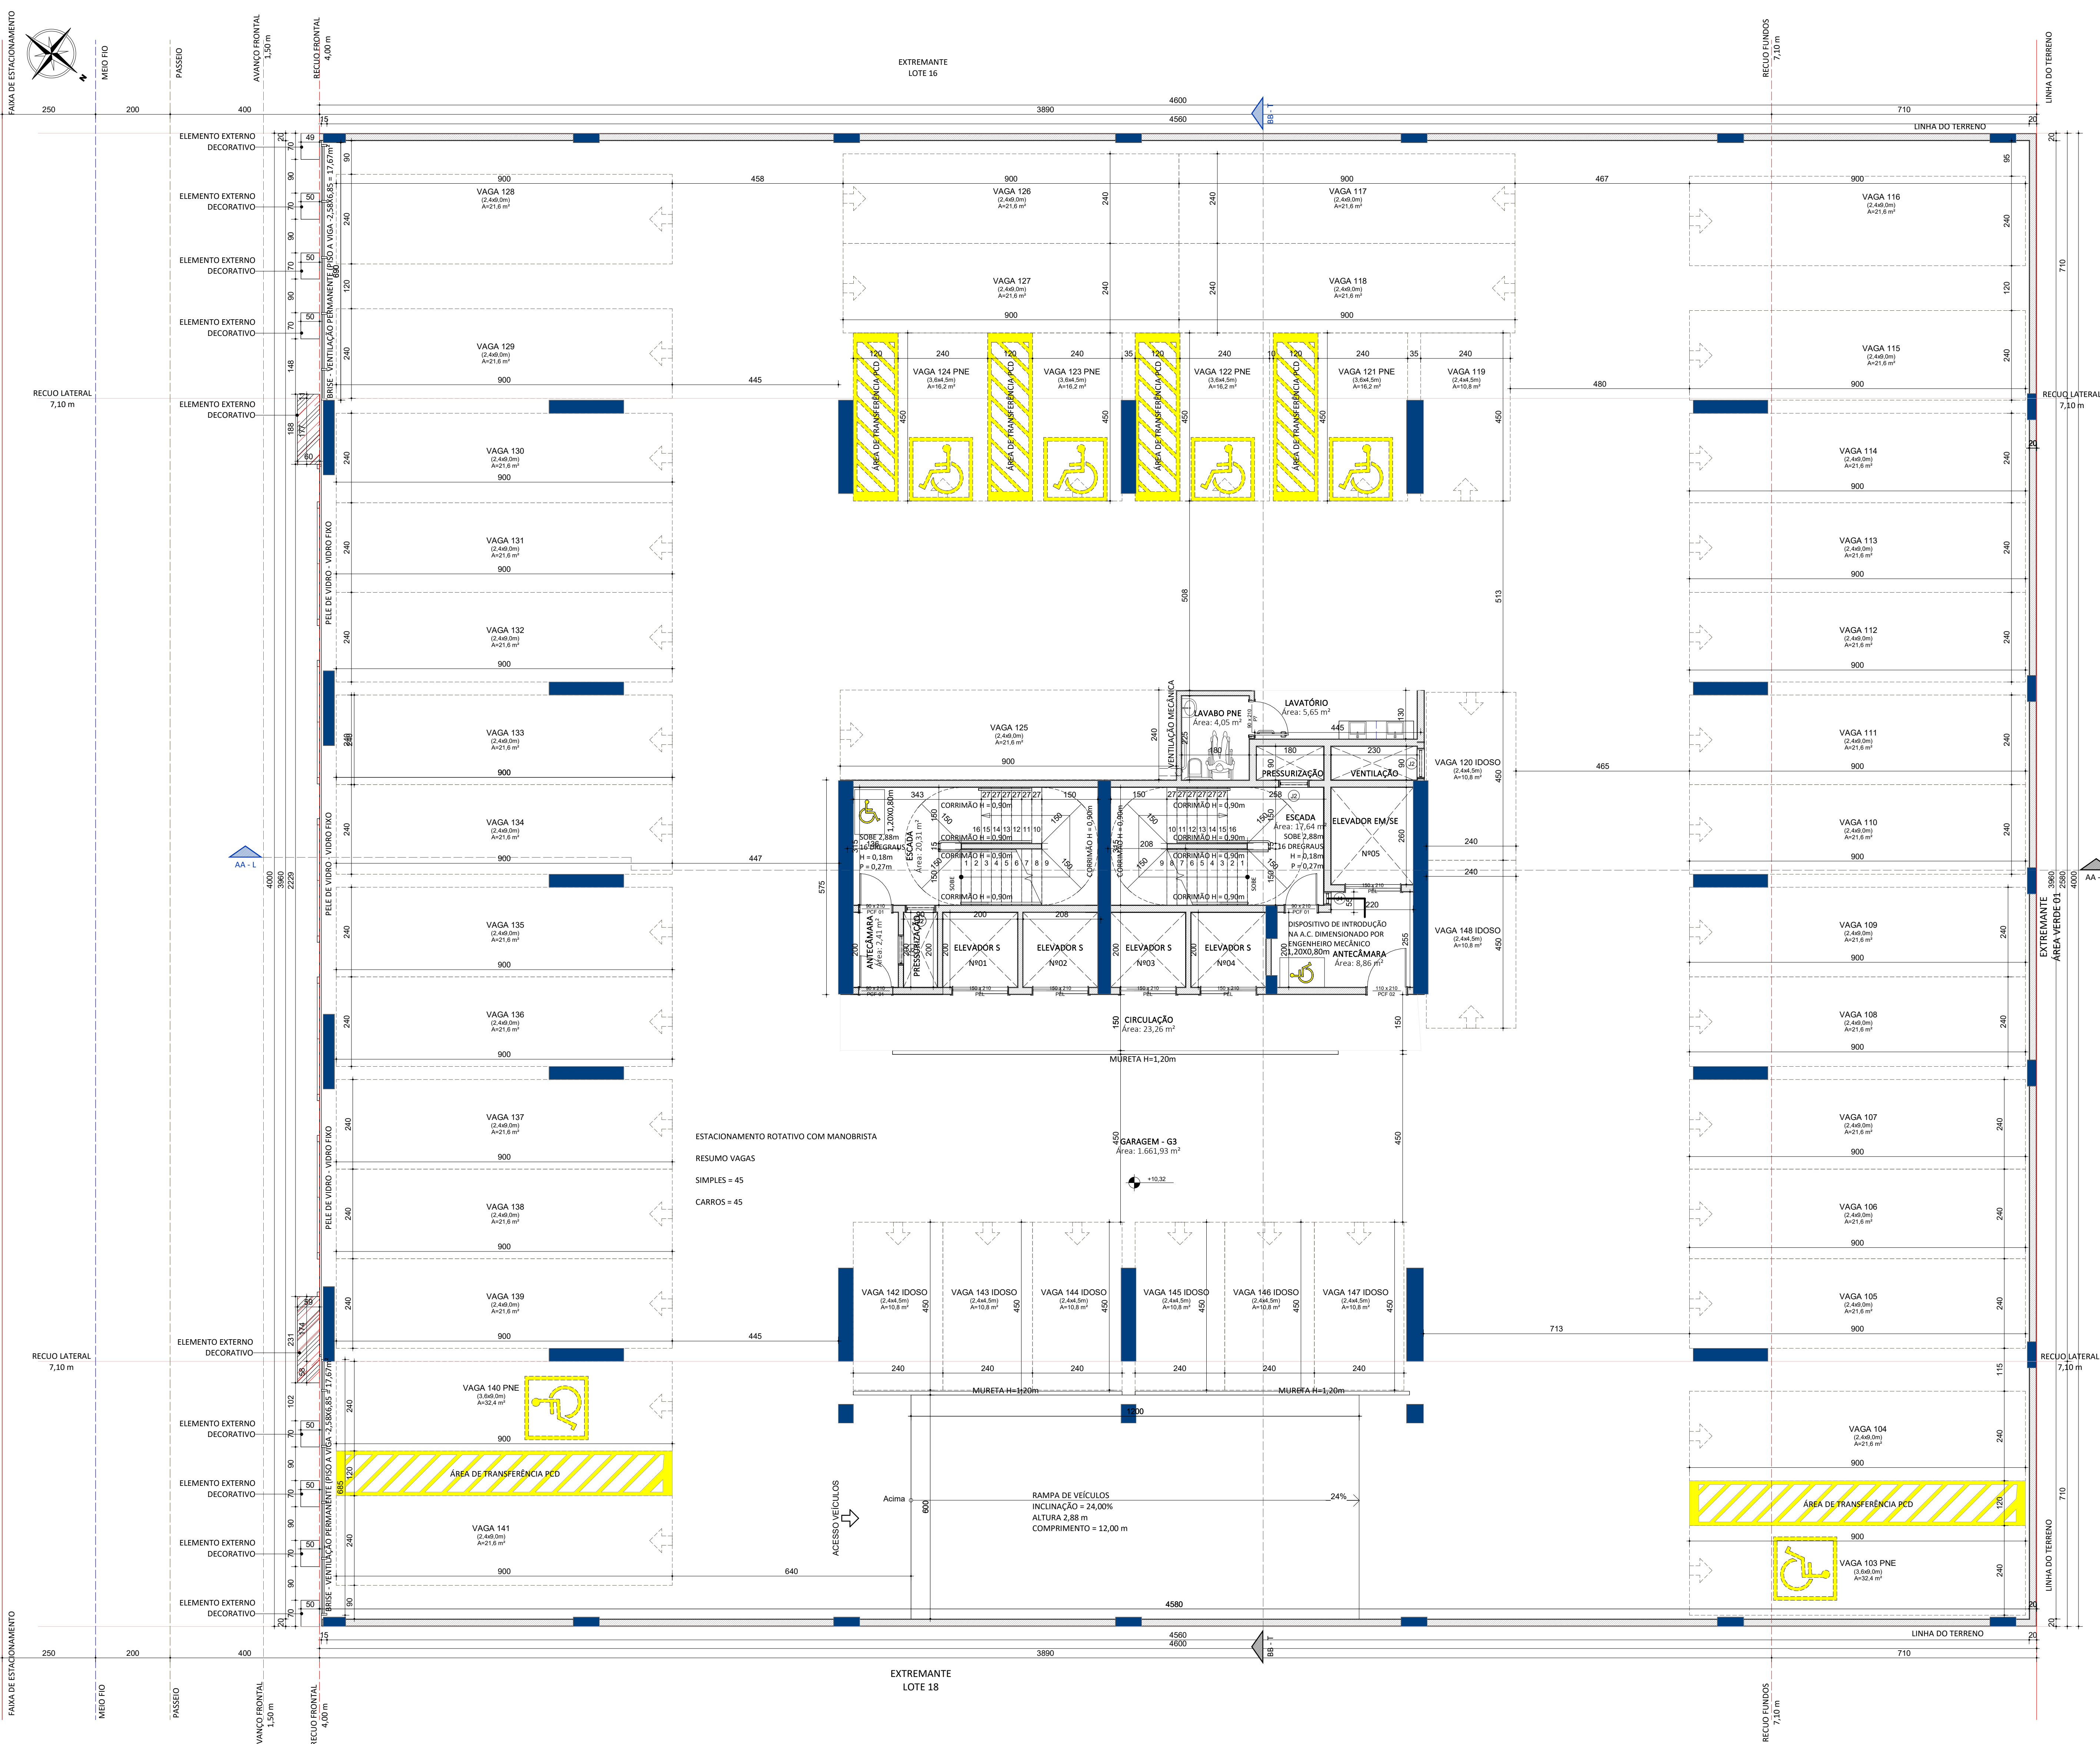

QUADRO DE JANELAS						
CÓD.	QT	COMPRIMENTO	ALTURA	PEITORIL	DESCRIÇÃO	ÁREA
J1	1	80	10	160	Esquadria de alumínio na cor branca / Janela gôlo (Acos). Vitrô acrílico	0,4 m²
J2	203	80	120	160	VENEZIANA ANTECÂMARA	0,96 m²
J3	51	80	80	150	JANELA MAXIMA AR - 1 FOLHA - ALUMÍNIO E VÍDRIO	0,64 m²
J4	32	80	120	160	VENEZIANA ANTECÂMARA - DIMENSIONADA ENG MEC	0,42 m²
J5	2	160	40	170	VENEZIANA VENTILADA	0,64 m²
J6	1	150	120	120	JANELA DE DESLIZAR - 2 FOLHAS - ALUMÍNIO E VÍDRIO	1,8 m²
J99						
J04	273	150	150	120	JANELA MAXIMA-AR - 1 FOLHA- ALU E VÍDRIO (ABERTURA 150x	2,25 m²

QUADRO DE VAGAS		
NÍVEL	QTDE	
PAV. 01 - TERREO	15	
PAV. 2 - GARAGEM G3	45	
PAV. 3 - GARAGEM G3	45	
PAV. 4 - GARAGEM G3	46	
PAV. 5 - GARAGEM G4	46	
PAV. 6 - GARAGEM G5	46	
	243	

REVISÃO	ASSUNTO	DESENHO	RESPONSÁVEL	DATA
R1	1º ANÁLISE	GIOVANNI D.	RS CONCEPT	11/11/2024



PROJETO

OBRA

ARQUITETÔNICO

LOTUS BUSINESS CENTER

RUA PROJETADA (AVENIDA RIO PEREQUE), Nº 539 - LOTE Nº 16 E LOTE Nº 17

LOTEAMENTO ANDORINHA CENTER, PORTO BELO SC

RESP. TÉCNICO

PROPRIETÁRIO

HÉCTOR RHAVI DA COSTA
CAU: A190987-8

L K NOVE EMPREENDIMENTOS IMOBILIÁRIOS SPE LTDA
CNPJ 44.023.808/1001-60

DATA 17/05/2024	OBRA TIPO EDIFÍCIO COMERCIAL E RESIDENCIAL MULTIFAMILIAR
PROTOCOLO RS 70.2021.1K9	CONTEÚDO PLANTA DO 4º PAVIMENTO GARAGEM - G3 QUADRO DE ESQUADRIAS
OBSERVAÇÕES IMPORTANTES: 1- Declaram que a aprovação do projeto não implica no reconhecimento por parte da Prefeitura de Minas Gerais do projeto de obra. 2- Declaram que as informações e os dados das áreas construídas nesse projeto, são verdadeiras e de sua responsabilidade e não de terceiros. 3- Declaram, como autor do projeto, que estão cientes de que foram atendidas as exigências contidas na Norma Brasileira de Edificações (NBR 15388/2003).	
ESCALA INDICADA	