
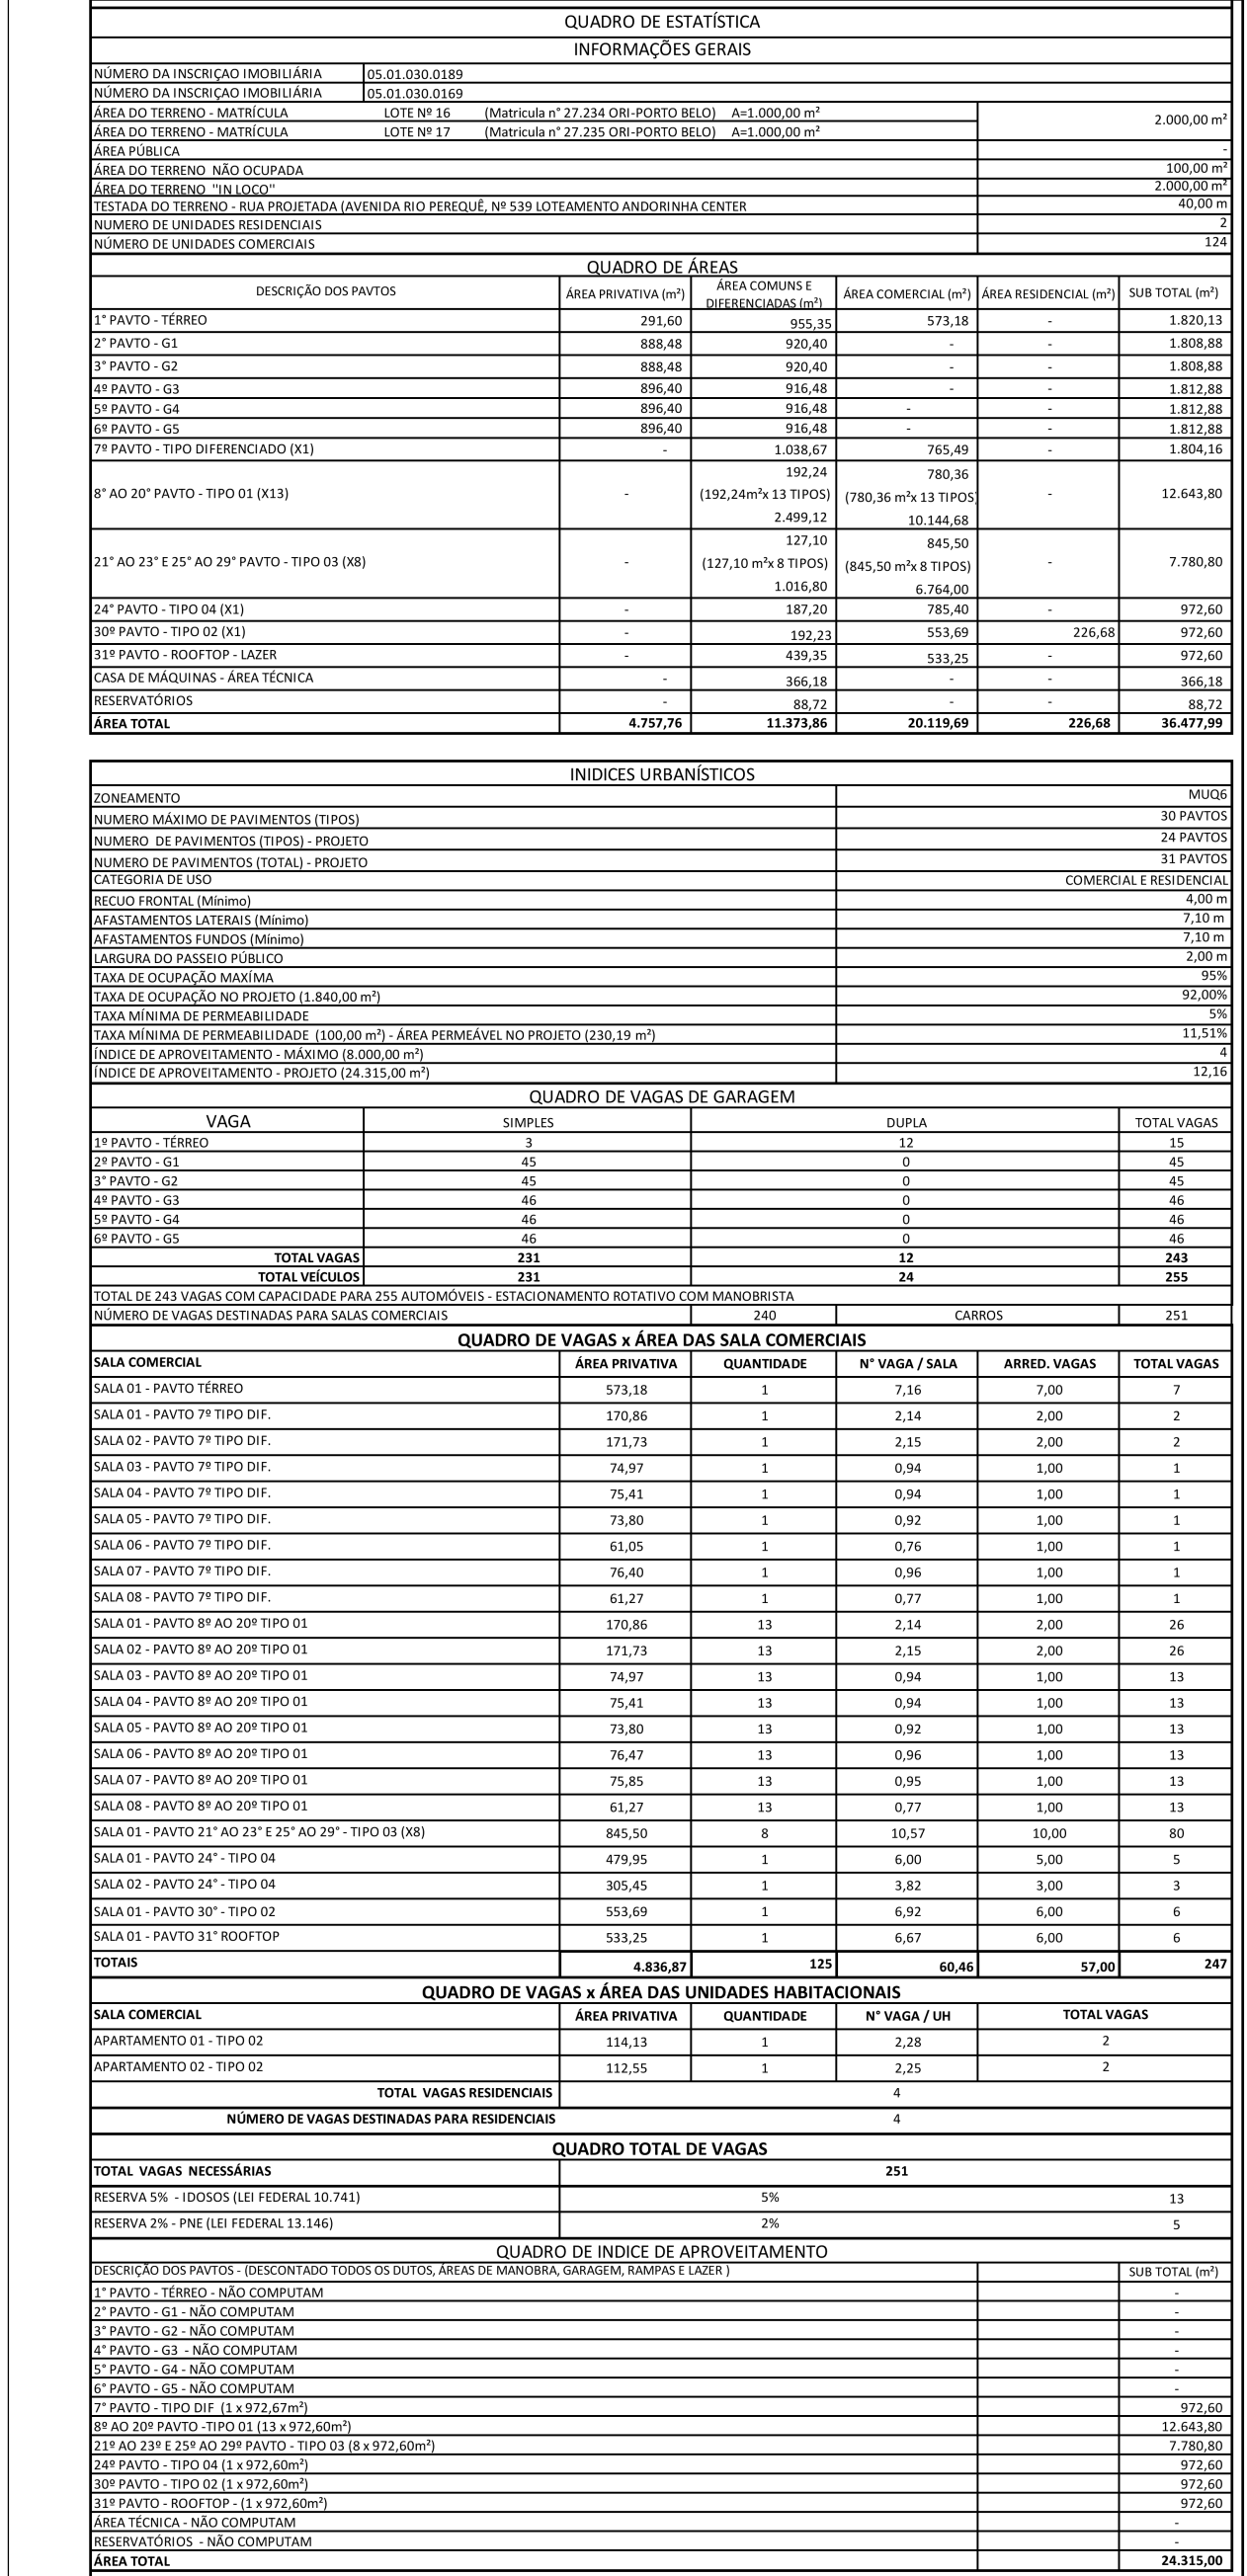
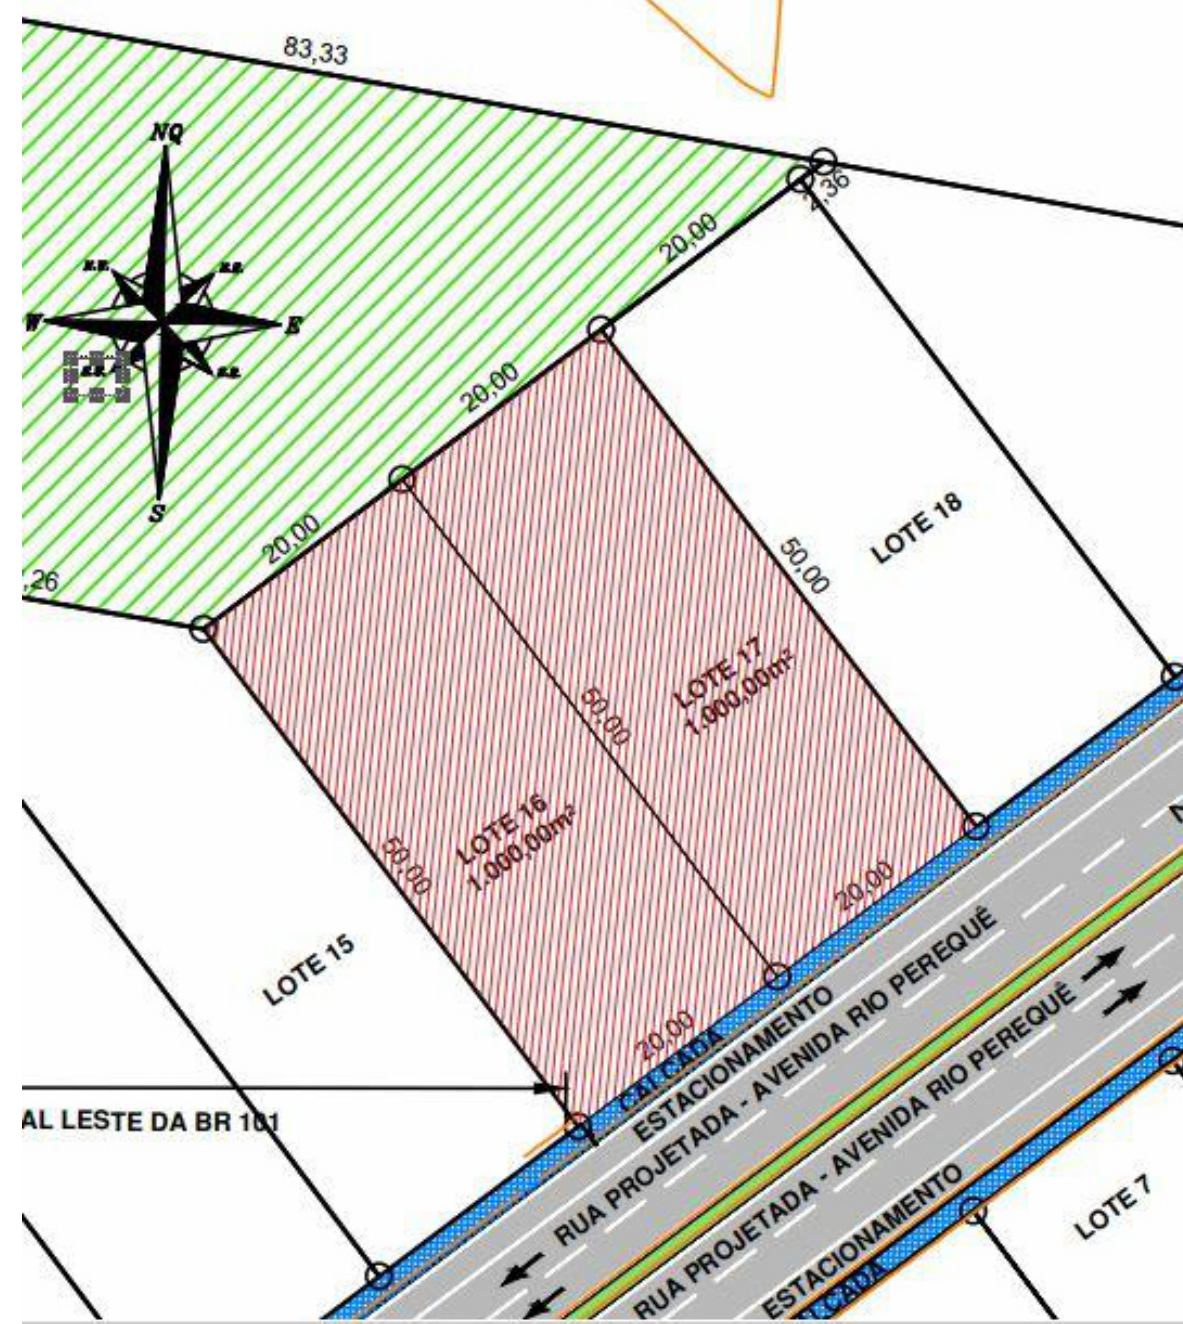
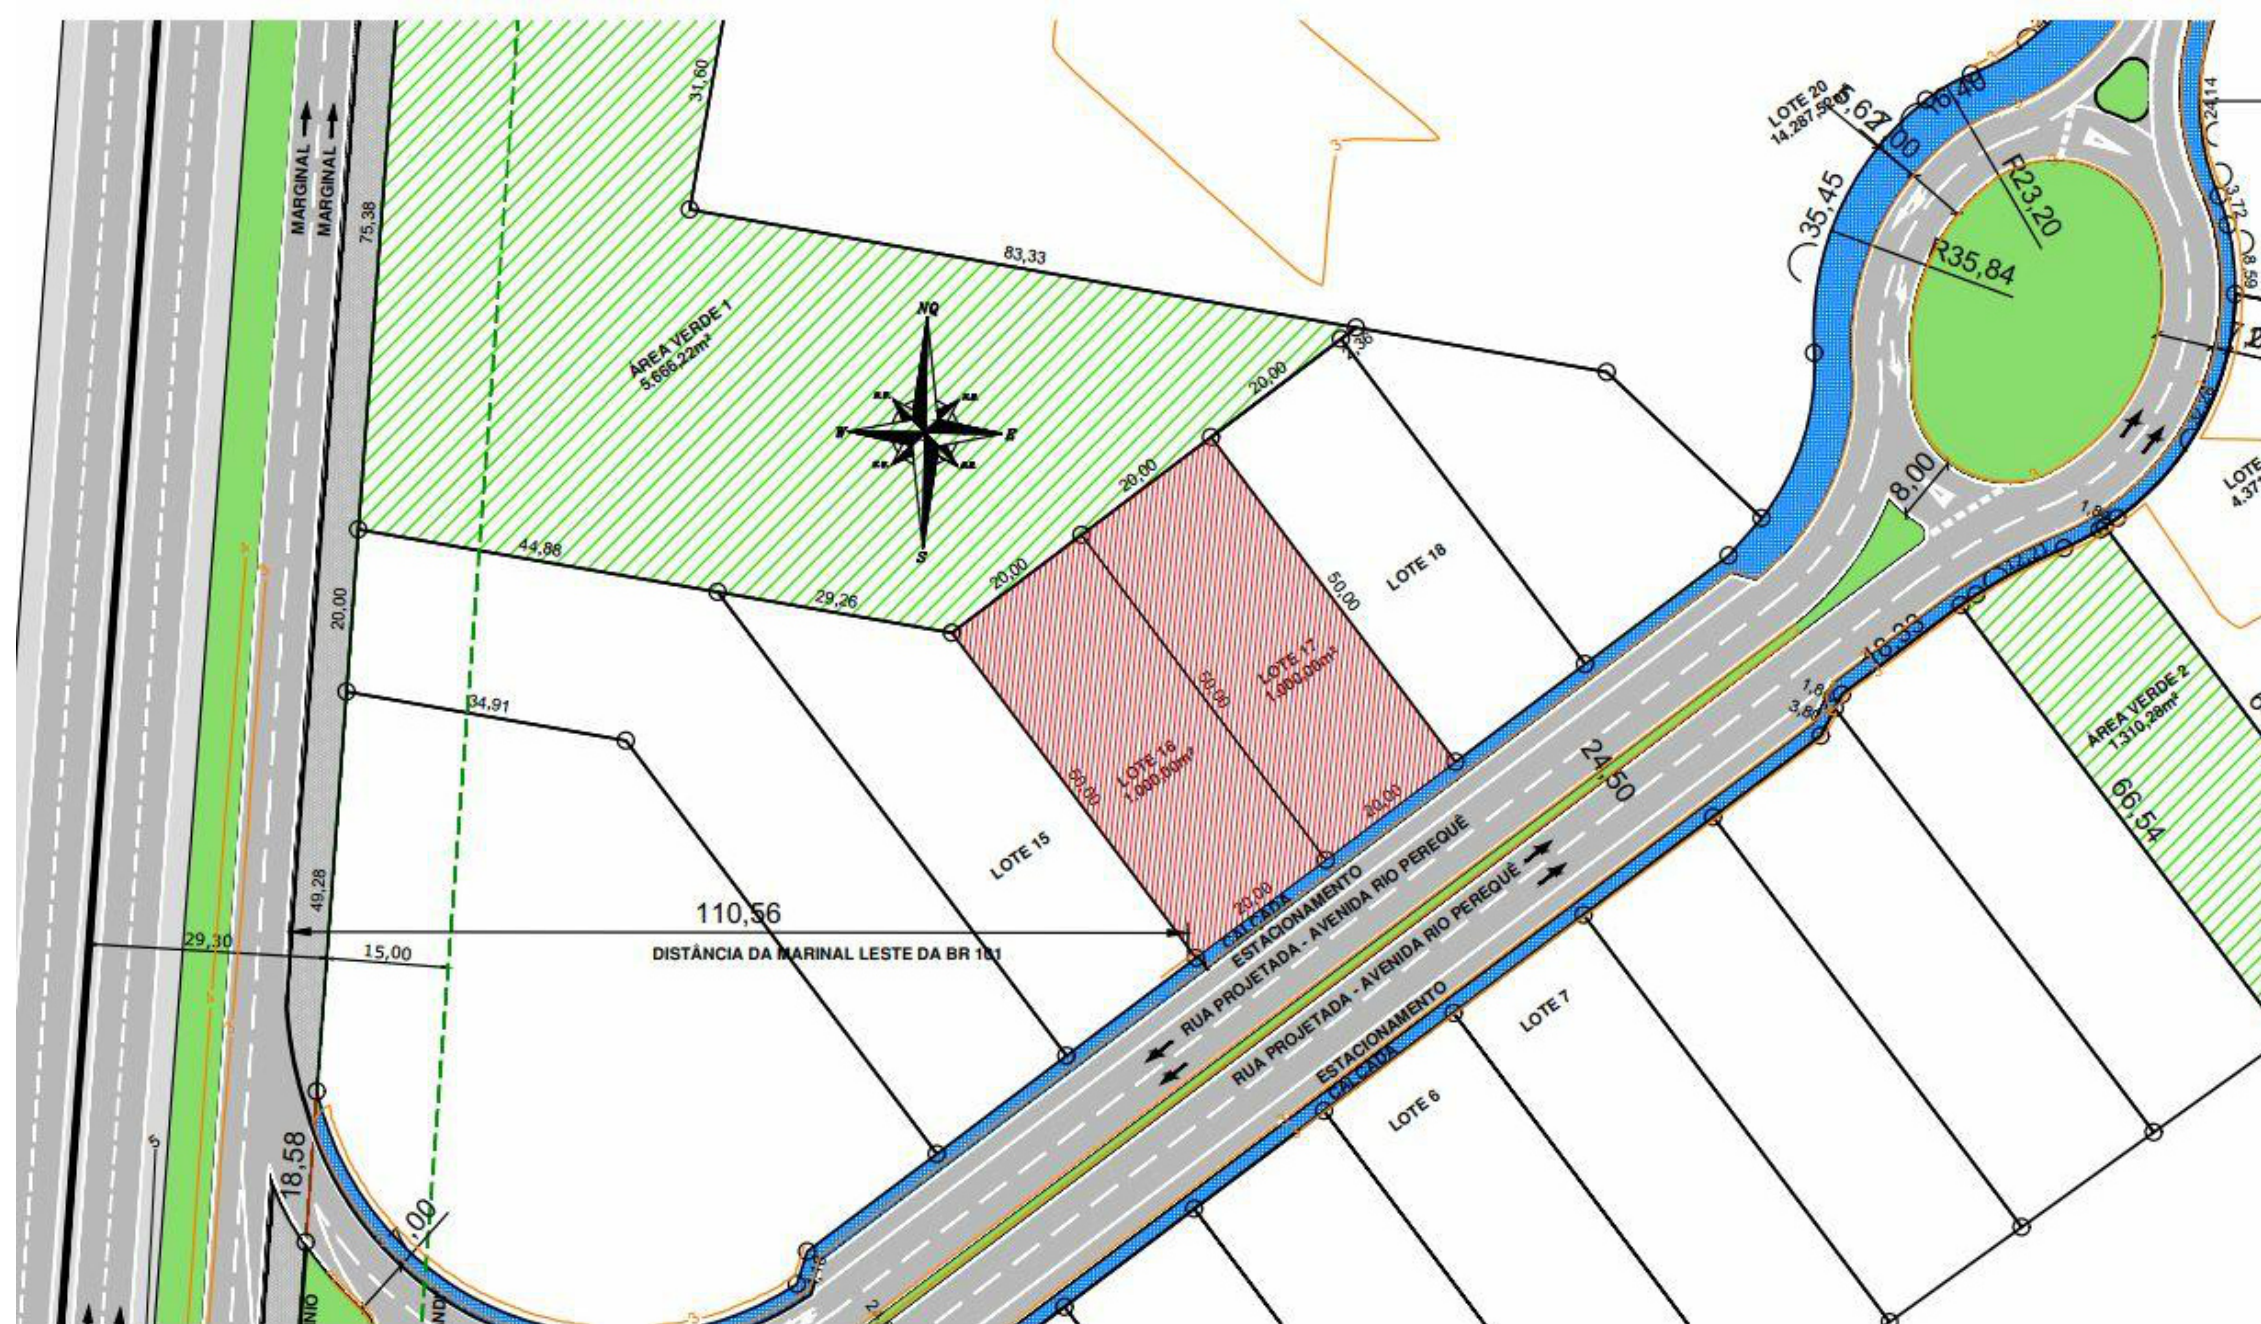


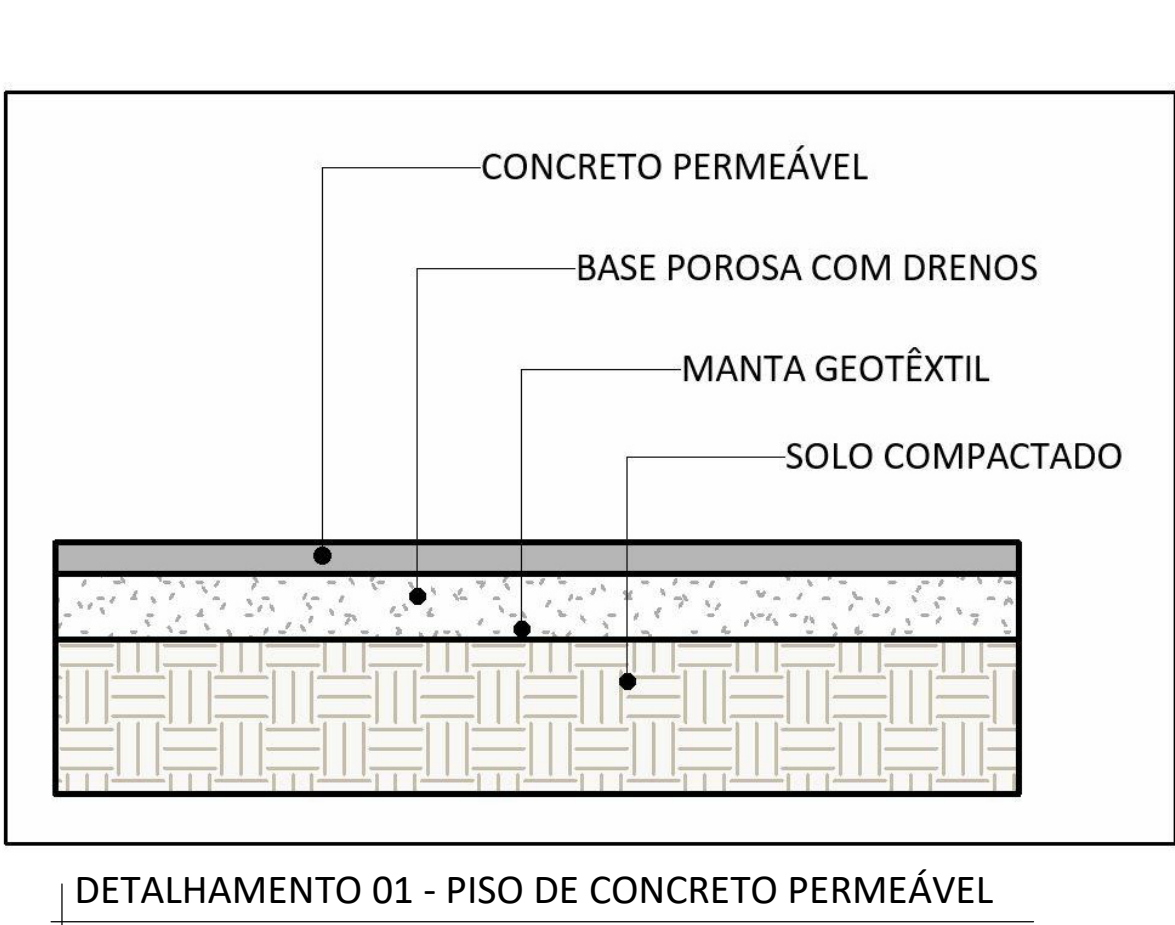

REVISÃO	ASSUNTO	DESENHO	RESPONSÁVEL	DATA

RS
CONCEPT

PROJETO

ARQUITETÔNICO

OBRA

LOTUS BUSINESS CENTER

RUA PROJETADA (AVENIDA RIO PEREQUÊ), N° 539 - LOTE N° 16 E LOTE N° 17
LOTEAMENTO ANDORINHA CENTER, PORTO BELO SC

RESP. TÉCNICO

HÉCTOR RHAÍVA DA COSTA
CAH: A190987-8

PROPRIETÁRIO

L K NOVE EMPREENDIMENTOS IMOBILIÁRIOS SPE LTDA
CNPJ 44.023.808/1001-60

DATA
17/05/2024

OBRA TIPO
EDIFÍCIO COMERCIAL E RESIDENCIAL MULTIFAMILIAR

PROTOCOLO RS
70.2021 LK9

CONTEÚDO
PLANTA DE SITUAÇÃO, PLANTA DE OCUPAÇÃO,
CORTE ESQUEMÁTICO SIMPLES, ESTATÍSTICA

OBSERVAÇÕES IMPORTANTES:

- Considera-se que a aprovação do projeto não implica no reconhecimento por parte da Prefeitura do direito de propriedade do terreno;
- Considera-se que as informações e os cálculos das áreas contidas neste projeto, são verdadeiras e de boa representação do local de terreno;
- Declara-se, como autor do projeto, que envio planas e que foram atendidas as exigências constantes da Norma Complementar de Edificações Habitação - ANEB 100/2015.

ESCALA
INDICADA

PRANCHAS

1
/ 21