


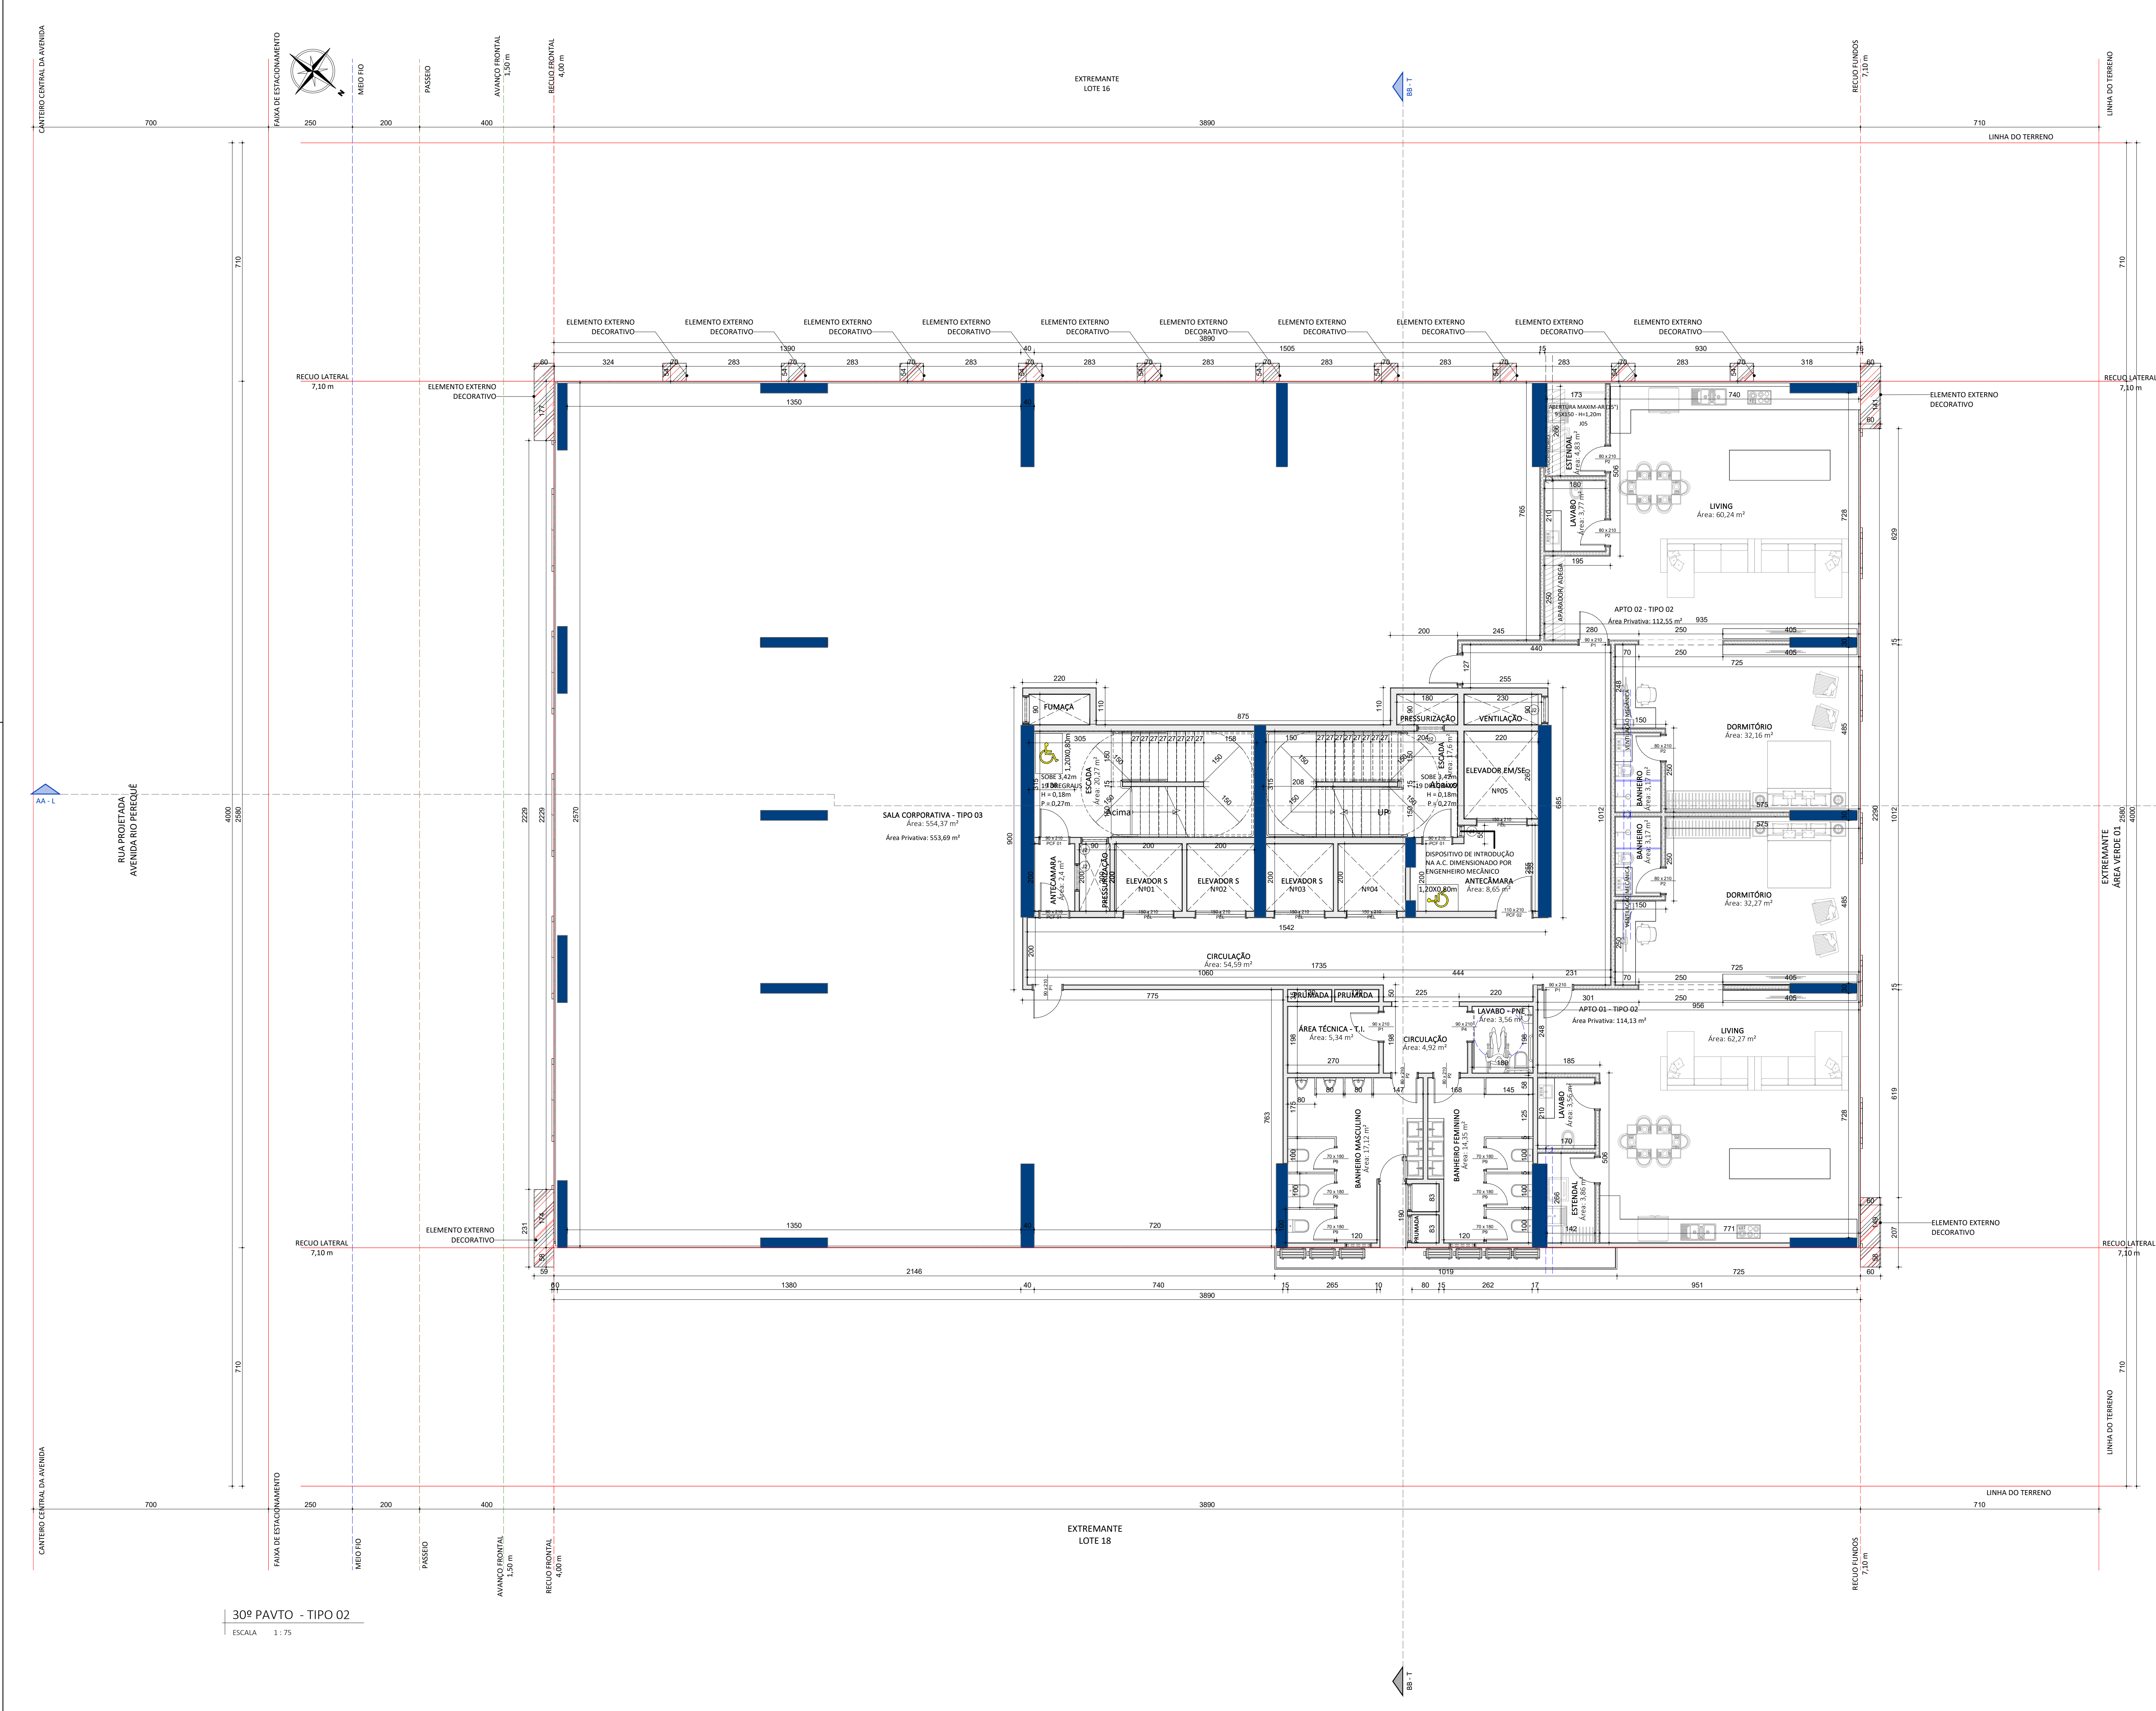

QUADRO DE JANELAS						
CÓD.	QT	COMPRIMENTO	ALTURA	PEITORIL	DESCRIÇÃO	ÁREA
J1	1	80	150	160	Esquadria de alumínio na cor branca / vidro gold (Acos). Vidro acústico	0,4 m²
J2	203	80	120	caimento	VENEZIANA ANTECÂMARA	0,96 m²
J3	51	80	80	150	JANELA MAXIM-AR - 1 FOLHA - ALUMÍNIO E VIDRO	0,64 m²
J4	32	80	120	caimento	VENEZIANA ANTECÂMARA - DIMENSIONADA ENG MRC	0,64 m²
J5	2	160	40	150	VENEZIANA VENTILADA	0,64 m²
J6	1	150	120	120	JANELA DE DESLIZAR - 2 FOLHAS - ALUMÍNIO E VIDRO	1,8 m²
J99	299					
J04	271	150	150	120	JANELA MAXIM-AR - 1 FOLHA - ALU E VIDRO (ABERTURA 150x	2,25 m²

QUADRO DE PORTAS				
CÓD	QT	COMPRIMENTO	ALTURA	DESCRIÇÃO
A25	6	160	210	Porta Dupla Interior de Giro
P1	155	90	210	PORTA DE GIRO - 1 FOLHA - MADEIRA
P2	56	80	210	PORTA DE GIRO - 1 FOLHA - MADEIRA
P3	1	70	210	PORTA DE GIRO - 1 FOLHA - MADEIRA
P4	25	90	210	PORTA DE DESLIZAR - 1 FOLHA - MADEIRA (PNE)
P5	6	90	210	PORTA DE GIRO - 1 FOLHA - VIDRO - SÓB MEDIDA
P6	1	720	210	PORTA DE ABIR - 1 FOLHA - MADEIRA (PNE)
P7	8	90	210	PORTA AUTOMÁTICA - VIDRO TEMPERADO
P8	2	350	300	PORTA AUTOMÁTICA - VIDRO TEMPERADO
P9	1	451	300	PORTA AUTOMÁTICA - VIDRO TEMPERADO
P10	150	70	180	PORTA DE GIRO - 1 FOLHA - SANITÁRIOS
P11	1	500	300	PORTA GARAGEM
P12	1	180	300	PORTA DE VIDRO - SÓB MEDIDA
P13	1	383	300	PORTA DE VIDRO - SÓB MEDIDA
P14	1	285	210	PORTA 1 FOLHA - ALUMÍNIO COM ANTRA ANTI-REFLEXO
P15	94	90	210	PORTA DE GIRO - 1 FOLHA - CORTA FOGO
P16	33	110	210	PORTA DE GIRO - 1 FOLHA - CORTA FOGO
P17	158	150	210	PORTA DO ELEVADOR
P18	1	350	300	PORTA GARAGEM
P19	5	130	210	PORTA VENEZIANA
P20	35	75	210	PORTA VENEZIANA
P21	2	80	120	PORTA VENEZIANA - VISTA

REVISÃO	ASSUNTO	DESENHO	RESPONSÁVEL	DATA
R1	1º ANÁLISE	GIOVANNI D.	RS CONCEPT	11/11/2024



RS
CONCEPT

PROJETO

OBRA

RESP. TÉCNICO

PROPRIETÁRIO

DATA

OBRA TIPO

PROTÓCOLO RS

CONTEÚDO

OBSERVAÇÕES IMPORTANTES:

ESCALA

INDICADA

12 / 21