

CANTERO CENTRAL DA AVENIDA

RUA PROJETADA
AVENIDA RIO PEREQUE

CANTERO CENTRAL DA AVENIDA

BARRILETE
ESCALA 1:75

FAMA DE ESTACIONAMENTO

MEIO FIO

PASSEIO

AVANÇO FRONTAL 1,50 m

RECULO FRONTAL 4,00 m

AA - L

RECULO LATERAL 7,10 m

RECULO LATERAL 7,10 m

MEIO FIO

PASSEIO

AVANÇO FRONTAL 1,50 m

RECULO FRONTAL 4,00 m

EXTREMANTE
LOTE 16

EXTREMANTE
LOTE 18

RECULO FUNDOS 7,10 m

LINHA DO TERRENO

EXTREMANTE
ÁREA VERDE 01

RECULO LATERAL 7,10 m


LINHA DO TERRENO

LINHA DO TERRENO

RECULO FUNDOS 7,10 m

QUADRO DE JANELAS						
CÓD.	QT	COMPRIMENTO	ALTURA	PEITORIL	DESCRIÇÃO	ÁREA
J1	1	80	150	160	Esquadria de alumínio na cor branca / folha gold (Alcos). Vidro acústico	0,6 m²
J2	203	80	120	carretilha	VENEZIANA ANTECÂMARA	0,96 m²
J3	51	80	80	150	JANELA MAXIM-AR - 1 FOLHA - ALUMÍNIO E VIDRO	0,64 m²
J4	32	80	120	carretilha	VENEZIANA ANTECÂMARA - DIMENSIONADA ENG MEC	0,64 m²
J5	2	160	40	170	VENEZIANA VENTILADA	0,64 m²
J6	1	150	120	120	JANELA DE DESLIZAR - 2 FOLHAS - ALUMÍNIO E VIDRO	1,8 m²
J95						
J04	271	150	150	120	JANELA MAXIM-AR - 1 FOLHA - ALU E VIDRO (ABERTURA 150x	2,25 m²

QUADRO DE PORTAS				
CÓD	QT	COMPRIMENTO	ALTURA	DESCRIÇÃO
A25	6	160	210	Porta Dobel Interior de Giro
P1	155	90	210	PORTA DE GIRO - 1 FOLHA - MADEIRA
P2	56	80	210	PORTA DE GIRO - 1 FOLHA - MADEIRA
P3	1	70	210	PORTA DE GIRO - 1 FOLHA - MADEIRA
P4	23	90	210	PORTA DE DESLIZAR - 1 FOLHA - MADEIRA (PNE)
P5	6	90	210	PORTA DE GIRO - 1 FOLHA - VIDRO - SOB MEDIDA
P6	1	720	210	
P7	8	90	210	PORTA DE ABIR - 1 FOLHA - MADEIRA (PNE)
P8	2	300	300	PORTA AUTOMÁTICA - VIDRO TEMPERADO
P9	1	451	300	PORTA AUTOMÁTICA - VIDRO TAMPAADO
P9	150	70	180	PORTA DE GIRO - 1 FOLHA - SANITÁRIOS
P10	1	500	300	PORTÃO GARAGEM
P11	1	180	300	PORTA DE VIDRO - SOB MEDIDA
P11	1	383	300	PORTA DE VIDRO - SOB MEDIDA
P101	1	280	210	PORTA 1 FOLHA - AUDITÓRIO CÂMARA ANTIFURTO
PCF 01	94	90	210	PORTA DE GIRO - 1 FOLHA - CORTA FOGO
PCF 02	31	110	210	PORTA DE GIRO - 1 FOLHA - CORTA FOGO
REL	108	150	210	PORTA DO ELEVADOR
P101	1	350	300	PORTÃO GARAGEM
VNZ 1	5	130	210	PORTA VENEZIANA
VNZ 2	35	75	210	PORTA VENEZIANA
VNZ 3	2	80	120	PORTA VENEZIANA - VISTA
	742			

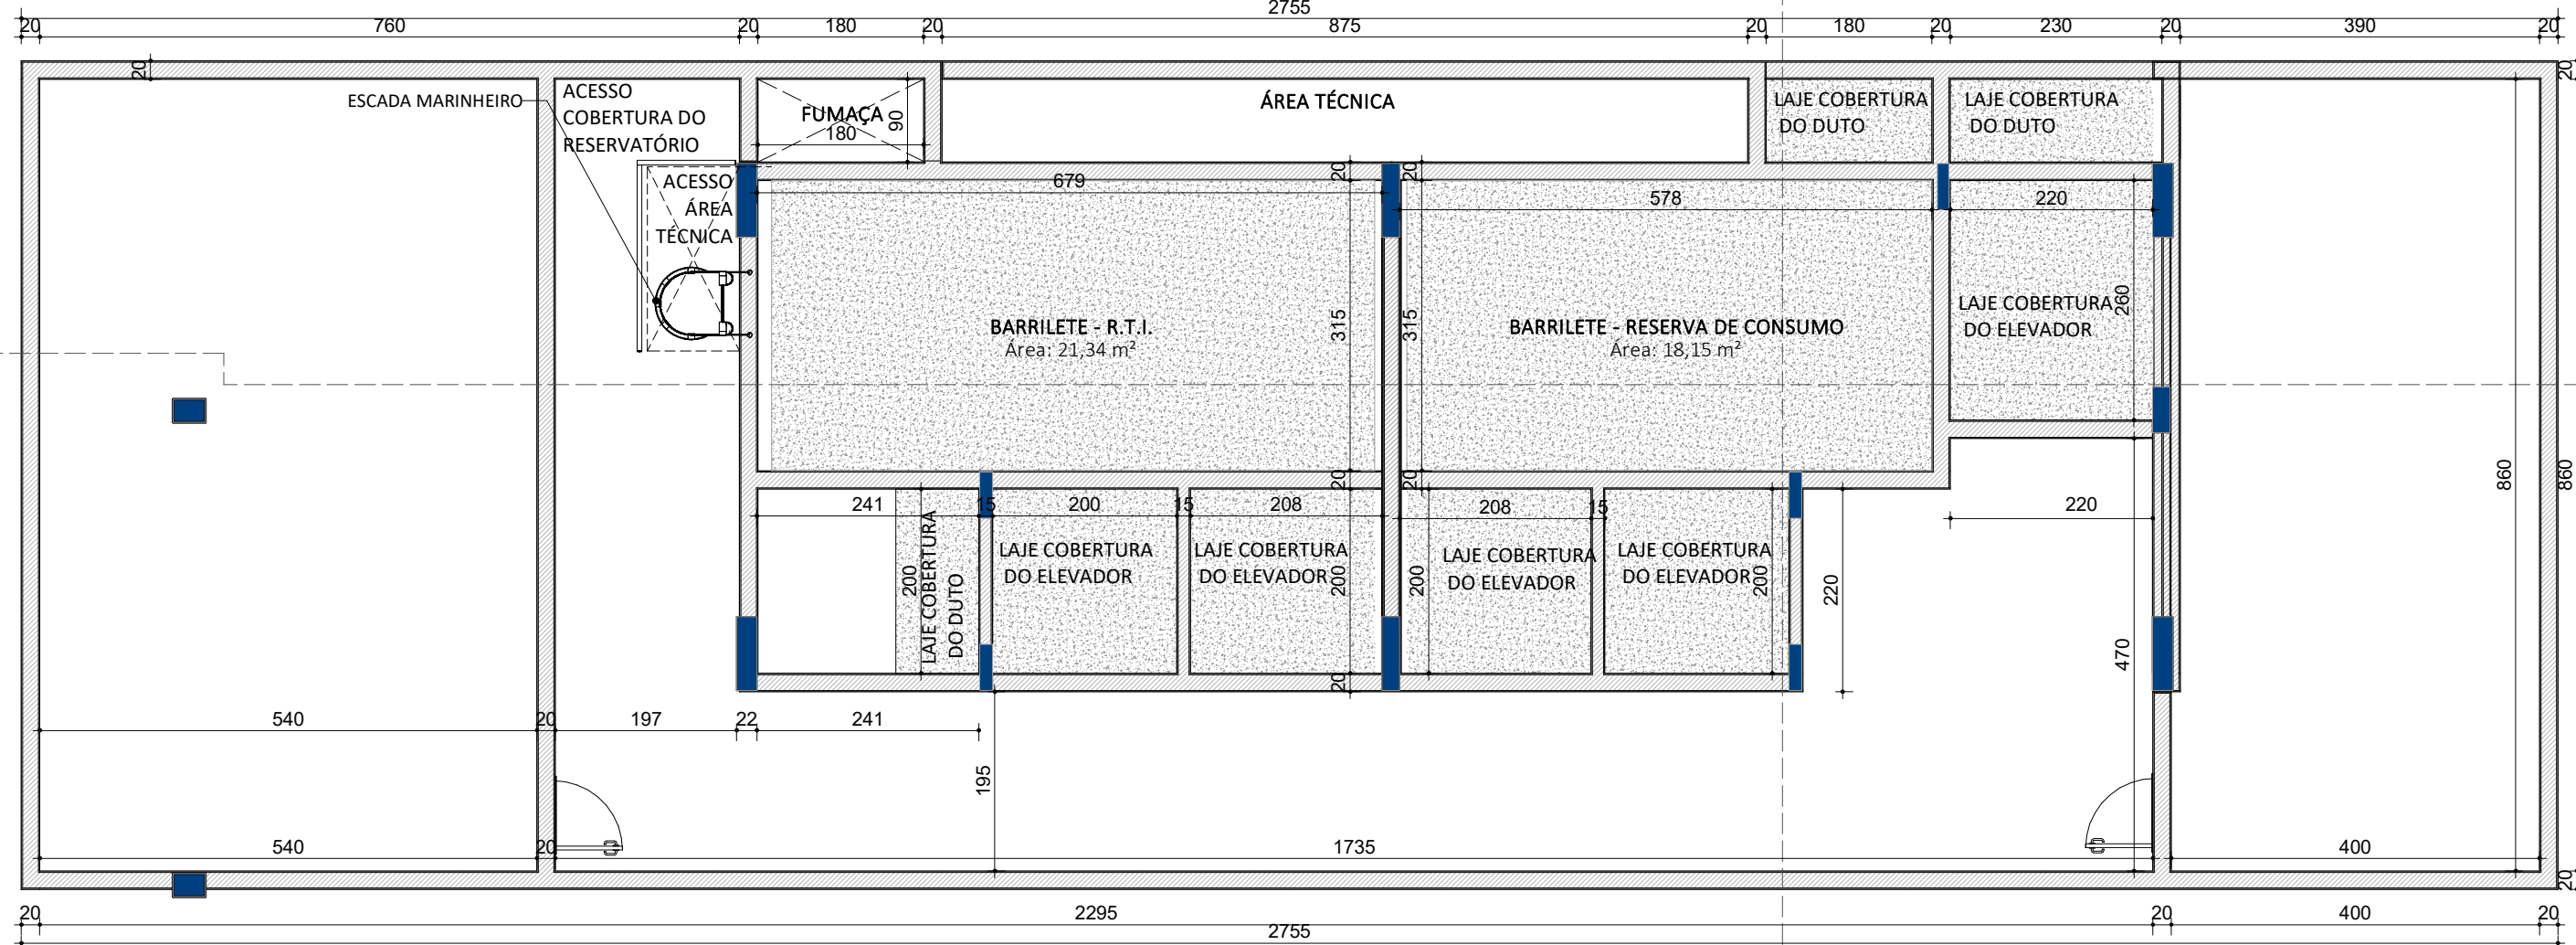

REVISÃO	ASSUNTO	DESENHO	RESPONSÁVEL	DATA
R1	1º ANÁLISE	GIOVANNI D.	RS CONCEPT	11/11/2024



PROJETO

OBRA

ARQUITETÔNICO

LOTUS BUSINESS CENTER

RUA PROJETADA (AVENIDA RIO PEREQUE), N° 539 - LOTE N° 16 E LOTE N° 17

LOTEAMENTO ANDORINHA CENTER, PORTO BELO SC

RESP. TÉCNICO	PROPRIETÁRIO
HÉCTOR RHAVI DA COSTA CAU: A190987-8	L K NOVE EMPREENDIMENTOS IMOBILIÁRIOS SPE LTDA CNPJ 44.023.808/1001-60

DATA	OBRA TIPO
17/05/2024	EDIFÍCIO COMERCIAL E RESIDENCIAL MULTIFAMILIAR
PROTOCOLO RS 70.2021 LK9	CONTEÚDO PLANTA BARRILETE QUADRO DE ESQUADRIAS

OBSERVAÇÕES IMPORTANTES:

I - Declaram que a elaboração do projeto não implica no reconhecimento por parte da Prefeitura do Brasil do planejamento do terreno.

II - Declaram que as informações e os cálculos das áreas contidas nesse projeto, são verdadeiras e de sua responsabilidade de acordo com a lei.

III - Declaram, como parte do projeto, que todos os dados e as informações fornecidas ao arquiteto constam no termo de prestação de serviços, assinado por ambos os lados.

IV - Declaram que o projeto foi elaborado de acordo com as normas técnicas de engenharia vigentes.

ESCALA INDICADA