


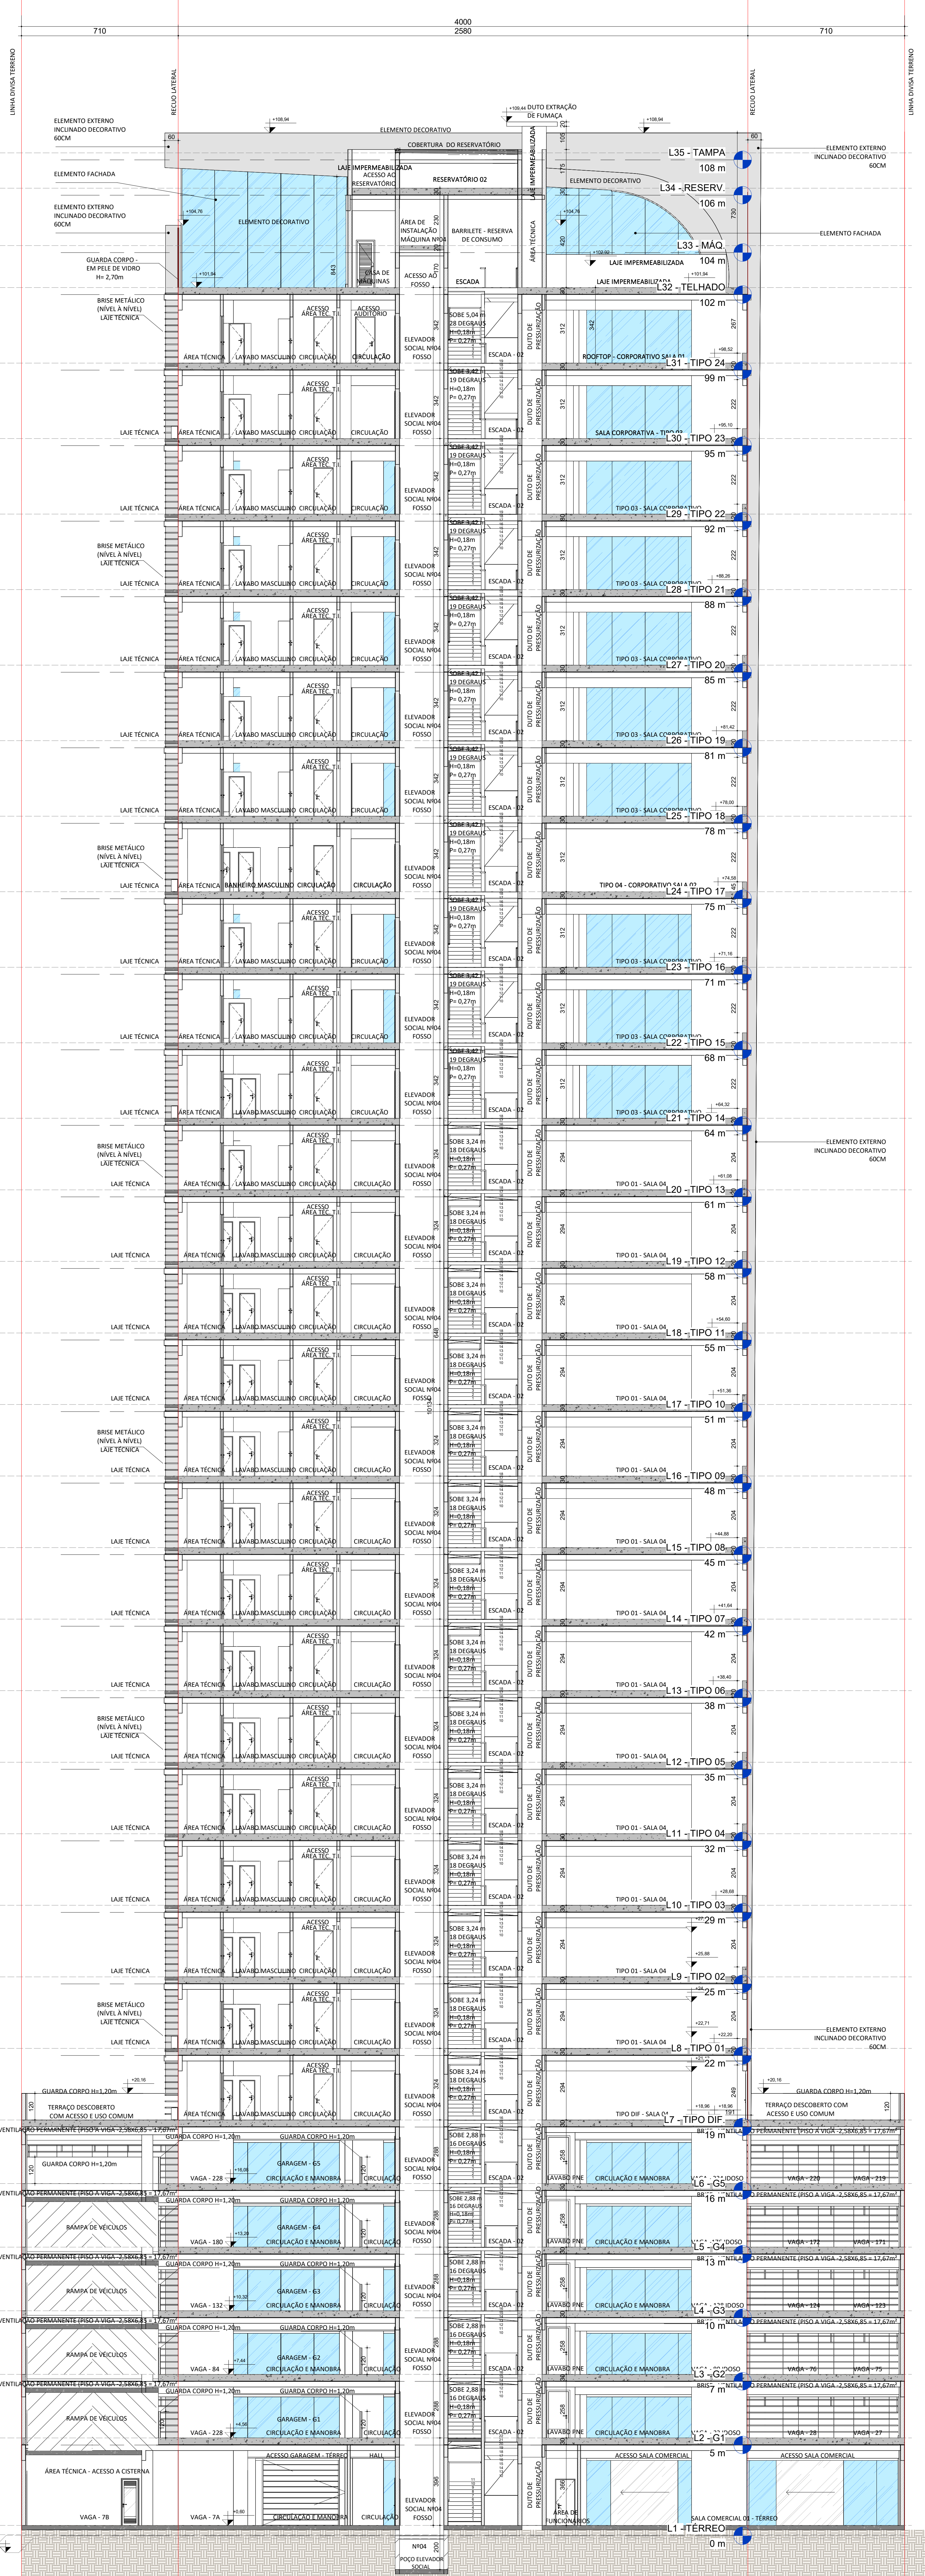

REVISÃO	ASSUNTO	DESENHO	RESPONSÁVEL	DATA
R1	1º ANÁLISE	GIOVANNI D.	RS CONCEPT	11/11/2024
 RS CONCEPT				
PROJETO				
OBRA				
LOTUS BUSINESS CENTER				
RUA PROJETADA (AVENIDA RIO PEREQUE), Nº 539 - LOTE Nº 16 E LOTE Nº 17				
LOTEAMENTO ANDORINHA CENTER, PORTO BELO SC				
RESP. TÉCNICO	HECTOR RHAVI DA COSTA CAU: A19087-6			
PROPRIETÁRIO	LX NOVE EMPREENDIMENTOS IMOBILIÁRIOS SPE LTDA CNPJ 44.023.808/1001-60			
DATA	17/05/2024	OBRA TIPO	EDIFÍCIO COMERCIAL E RESIDENCIAL MULTIFAMILIAR	
PROTOCOLO RS	70.2023 LK9	CONTEÚDO	CORTE TRANSVERSAL - BB	
OBSERVAÇÕES IMPORTANTES:		ESCALA INDICADA		

www.rsconcept.com.br
rs@rsconcept.com.br

Fone: (47) 3368 8110

Rua 292, nº 201 | sala 01 | lapasm/SC

FRANCHA

19
/ 21