


CANTERO CENTRAL DA AVENIDA

RUA PROJETADA
AVENIDA RIO PEREQUE

CANTERO CENTRAL DA AVENIDA

2º PAVTO - GARAGEM G1

ESCALA 1:75

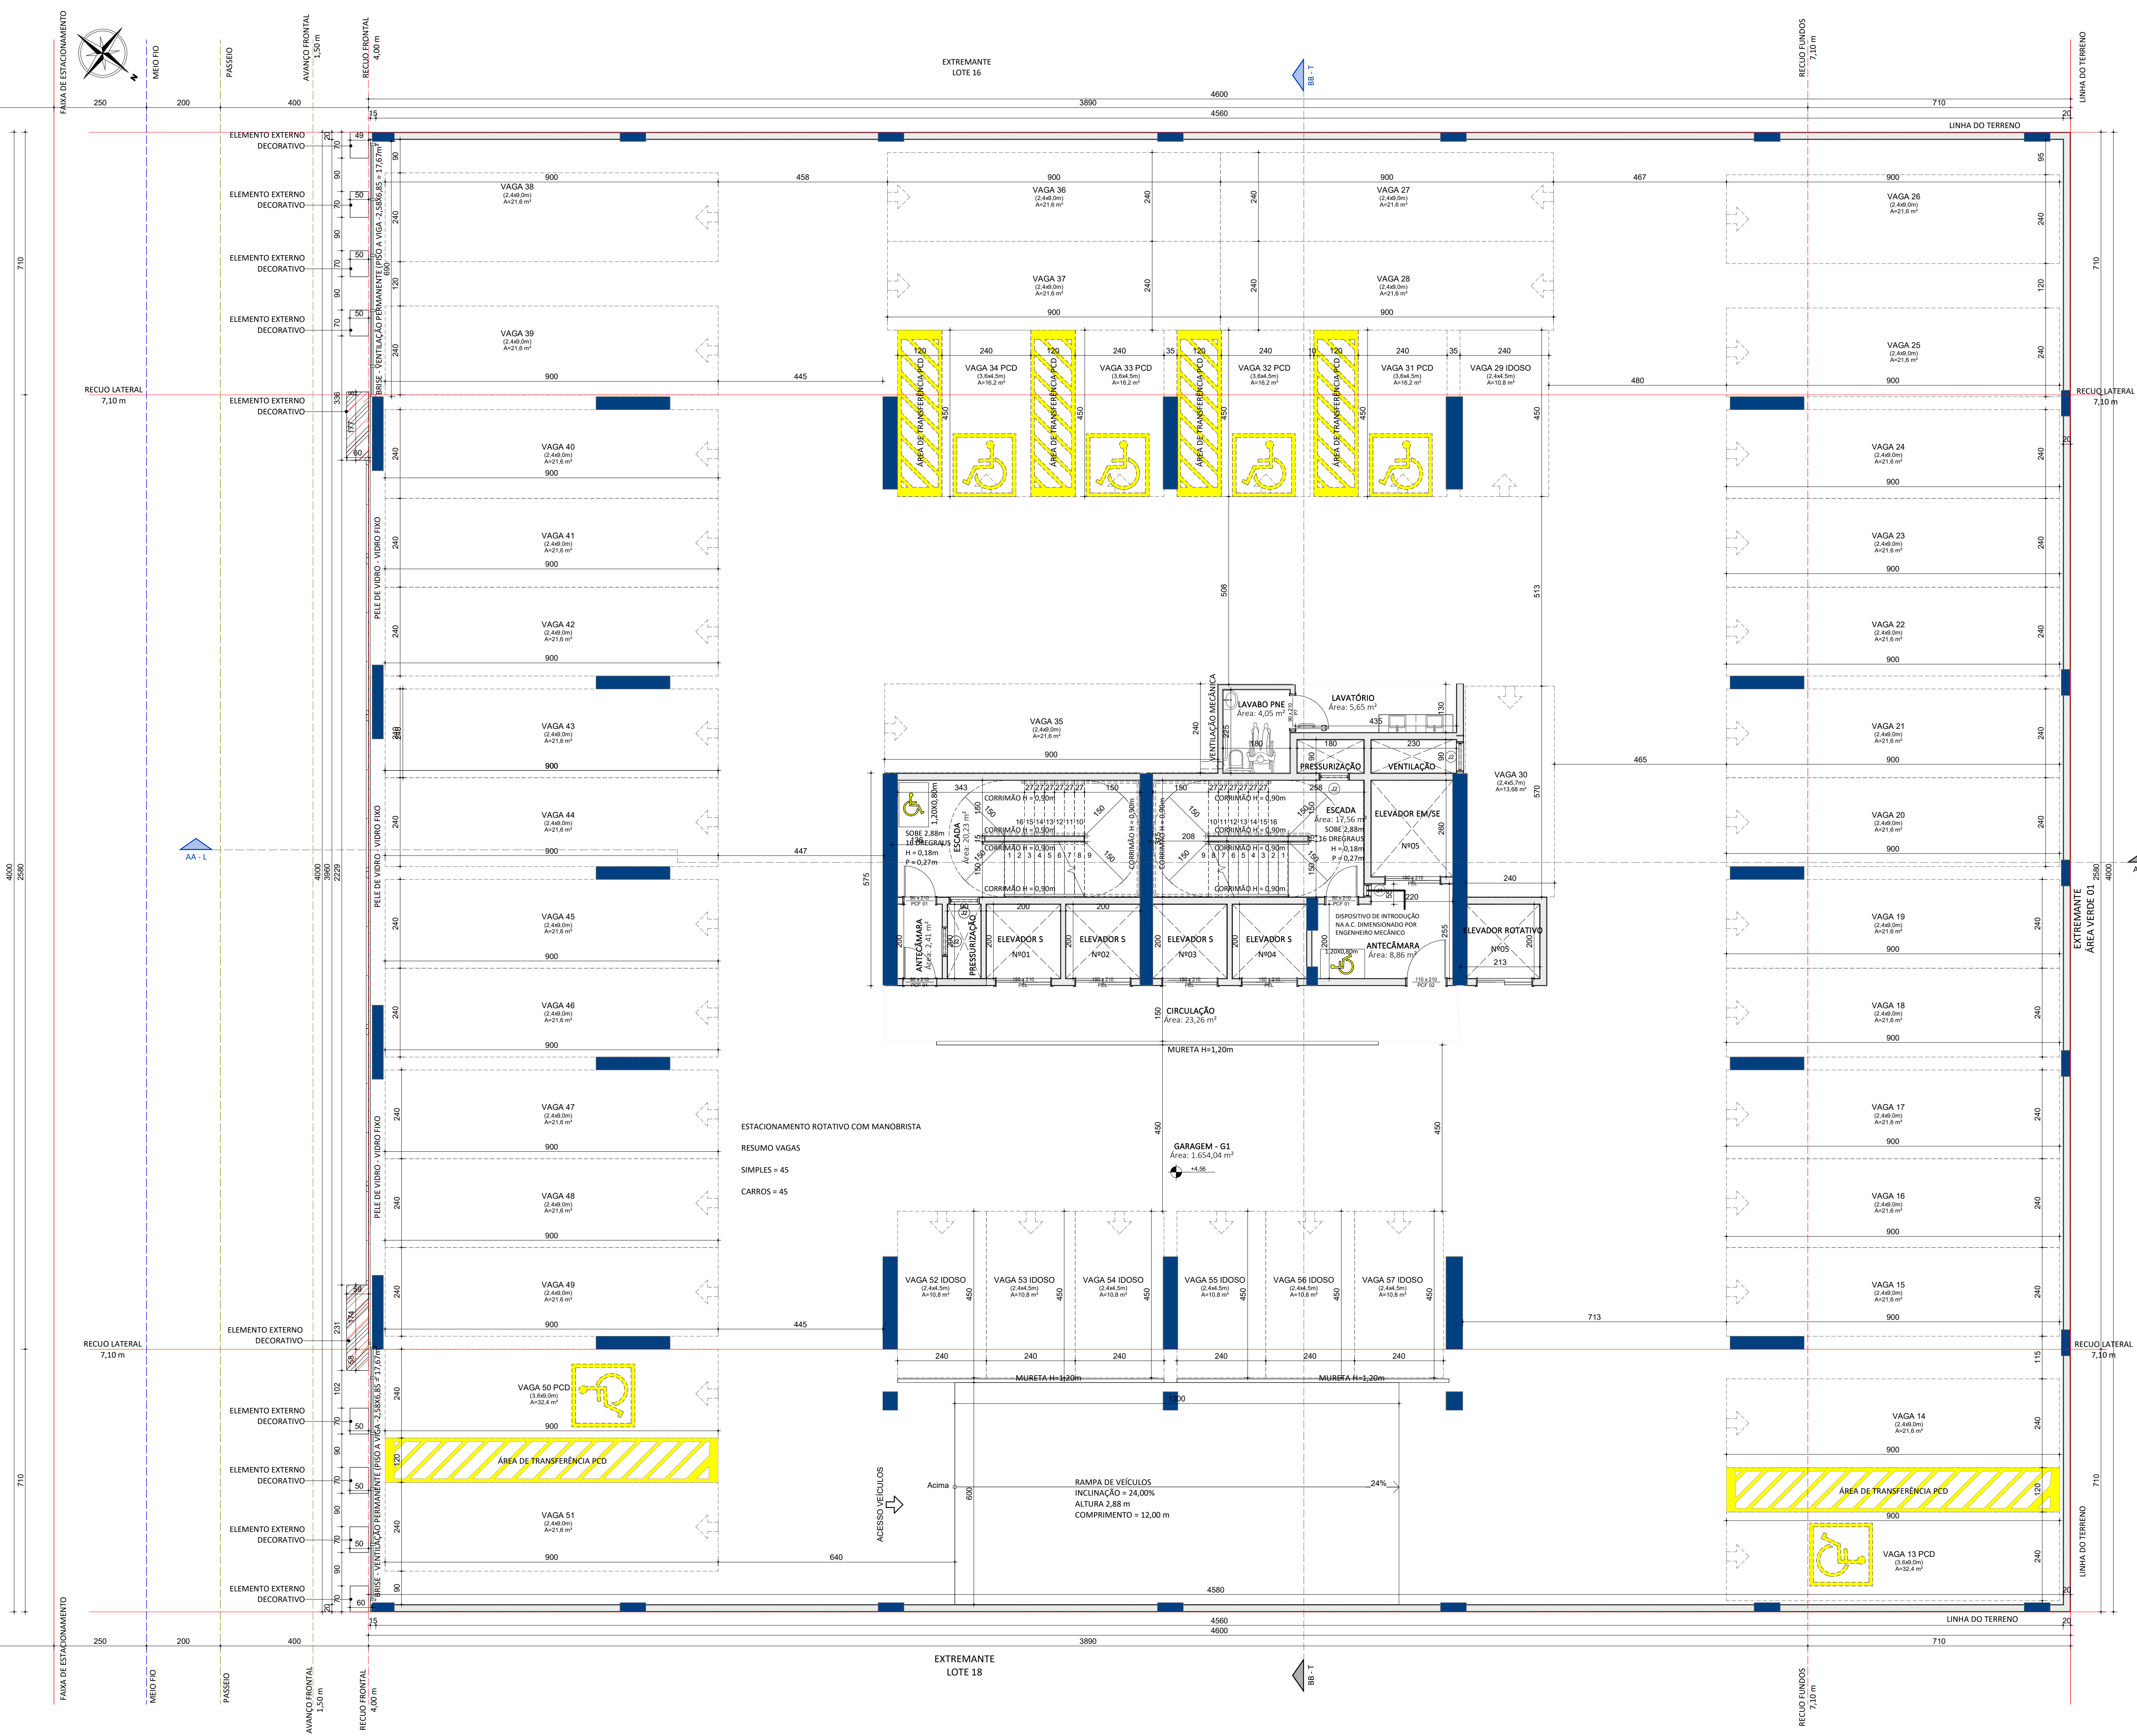

QUADRO DE JANELAS						
CÓD.	QT	COMPRIMENTO	ALTURA	PEITORIL	DESCRIÇÃO	ÁREA
J1	1	80	150	160	Esquadria de alumínio na cor branca / vidro gold (Acos). Vidro acústico	0,4 m²
J2	201	80	120	varretero	VENEZIANA ANTECAMARA	0,96 m²
J3	51	80	80	150	JANELA MAXIMA AR - 1 FOLHA - ALUMÍNIO E VIDRO	0,64 m²
J4	32	80	120	varretero	VENEZIANA ANTECAMARA - DIMENSIONADA ENG MEC	0,64 m²
J5	2	160	40	150	VENEZIANA VENTILADA	0,64 m²
J6	1	150	120	120	JANELA DE DESLIZAR - 2 FOLHAS - ALUMÍNIO E VIDRO	1,8 m²
J04	271	150	150	120	JANELA MAXIM-AR - 1 FOLHA - ALU E VIDRO (ABERTURA 150x	2,25 m²

QUADRO DE PORTAS				
CÓD	QT	COMPRIMENTO	ALTURA	DESCRIÇÃO
A25	6	160	210	Porta Dupla Interior de Giro
P1	155	90	210	PORTA DE GIRO - 1 FOLHA - MADEIRA
P2	56	80	210	PORTA DE GIRO - 1 FOLHA - MADEIRA
P3	1	70	210	PORTA DE GIRO - 1 FOLHA - MADEIRA
P4	25	90	210	PORTA DE DESLIZAR - 1 FOLHA - MADEIRA (PNE)
P5	6	90	210	PORTA DE GIRO - 1 FOLHA - VIDRO - SOB MEDIDA
P6	1	720	210	PORTA DE ABIR - 1 FOLHA - MADEIRA (PNE)
P7	8	90	210	PORTA AUTOMÁTICA - VIDRO TEMPERADO
P8	2	300	300	PORTA AUTOMÁTICA - VIDRO TEMPERADO
P9	1	451	300	PORTA AUTOMÁTICA - VIDRO TEMPERADO
P10	150	70	180	PORTA DE GIRO - 1 FOLHA - SANITÁRIOS
P10	1	500	300	PORTA GARAGEM
P11	1	100	300	PORTA DE VIDRO - SOB MEDIDA
P11	1	383	300	PORTA DE VIDRO - SOB MEDIDA
P101	1	158	150	PORTA 1 FOLHA - ALUMÍNIO COM ANTRA ANTI-PANICO
PC1	94	90	210	PORTA DE GIRO - 1 FOLHA - CORTA FOGO
PC1	31	110	210	PORTA DE GIRO - 1 FOLHA - CORTA FOGO
REL	158	150	210	PORTA DO ELEVADOR
P101	1	350	300	PORTA GARAGEM
VW1	5	130	210	PORTA VENEZIANA
VW2	35	70	210	PORTA VENEZIANA
VW3	2	80	120	PORTA VENEZIANA - VISTA
	742			

QUADRO DE VAGAS	
NÍVEL	QTDE
PAV. 01 - TERREO	15
PAV. 2 - GARAGEM G2	45
PAV. 3 - GARAGEM G3	45
PAV. 4 - GARAGEM G4	46
PAV. 5 - GARAGEM G5	46
PAV. 6 - GARAGEM G6	46
	243

REVISÃO	ASSUNTO	DESENHO	RESPONSÁVEL	DATA
R1	1º ANÁLISE	GIOVANNI D.	RS CONCEPT	11/11/2024



ARQUITETÔNICO

LOTUS BUSINESS CENTER
RUA PROJETADA (AVENIDA RIO PEREQUE), Nº 539 - LOTE Nº 16 E LOTE Nº 17
LOTEAMENTO ANDORINHA CENTER, PORTO BELO SC

RESP. TÉCNICO	PROPRIETÁRIO
HÉCTOR RHAVI DA COSTA CAU: A190987-8	L K NOVE EMPREENDIMENTOS IMOBILIÁRIOS SPE LTDA CNPJ 44.023.808/1001-60

DATA	OBRA TIPO
17/05/2024	EDIFÍCIO COMERCIAL E RESIDENCIAL MULTIFAMILIAR
PROTOCOLO RS	CONTEÚDO
70.2021.1K9	PLANTA DO 2º PAVIMENTO GARAGEM - G1 QUADRO DE ESQUADRIAS

OBSERVAÇÕES IMPORTANTES:
1. Declaram que a aprovação do projeto não implica no reconhecimento por parte da Prefeitura de
Belo Horizonte do terreno.
2. Declaram que as informações e os dados das áreas contidas nesse projeto, são verdadeiras e de
sua responsabilidade de obter no terreno.
3. Declaram, como autor do projeto, que estão cientes e que assumem a responsabilidade de qualquer alteração
na forma construída em relação às informações contidas no projeto.
ESCALA INDICADA