
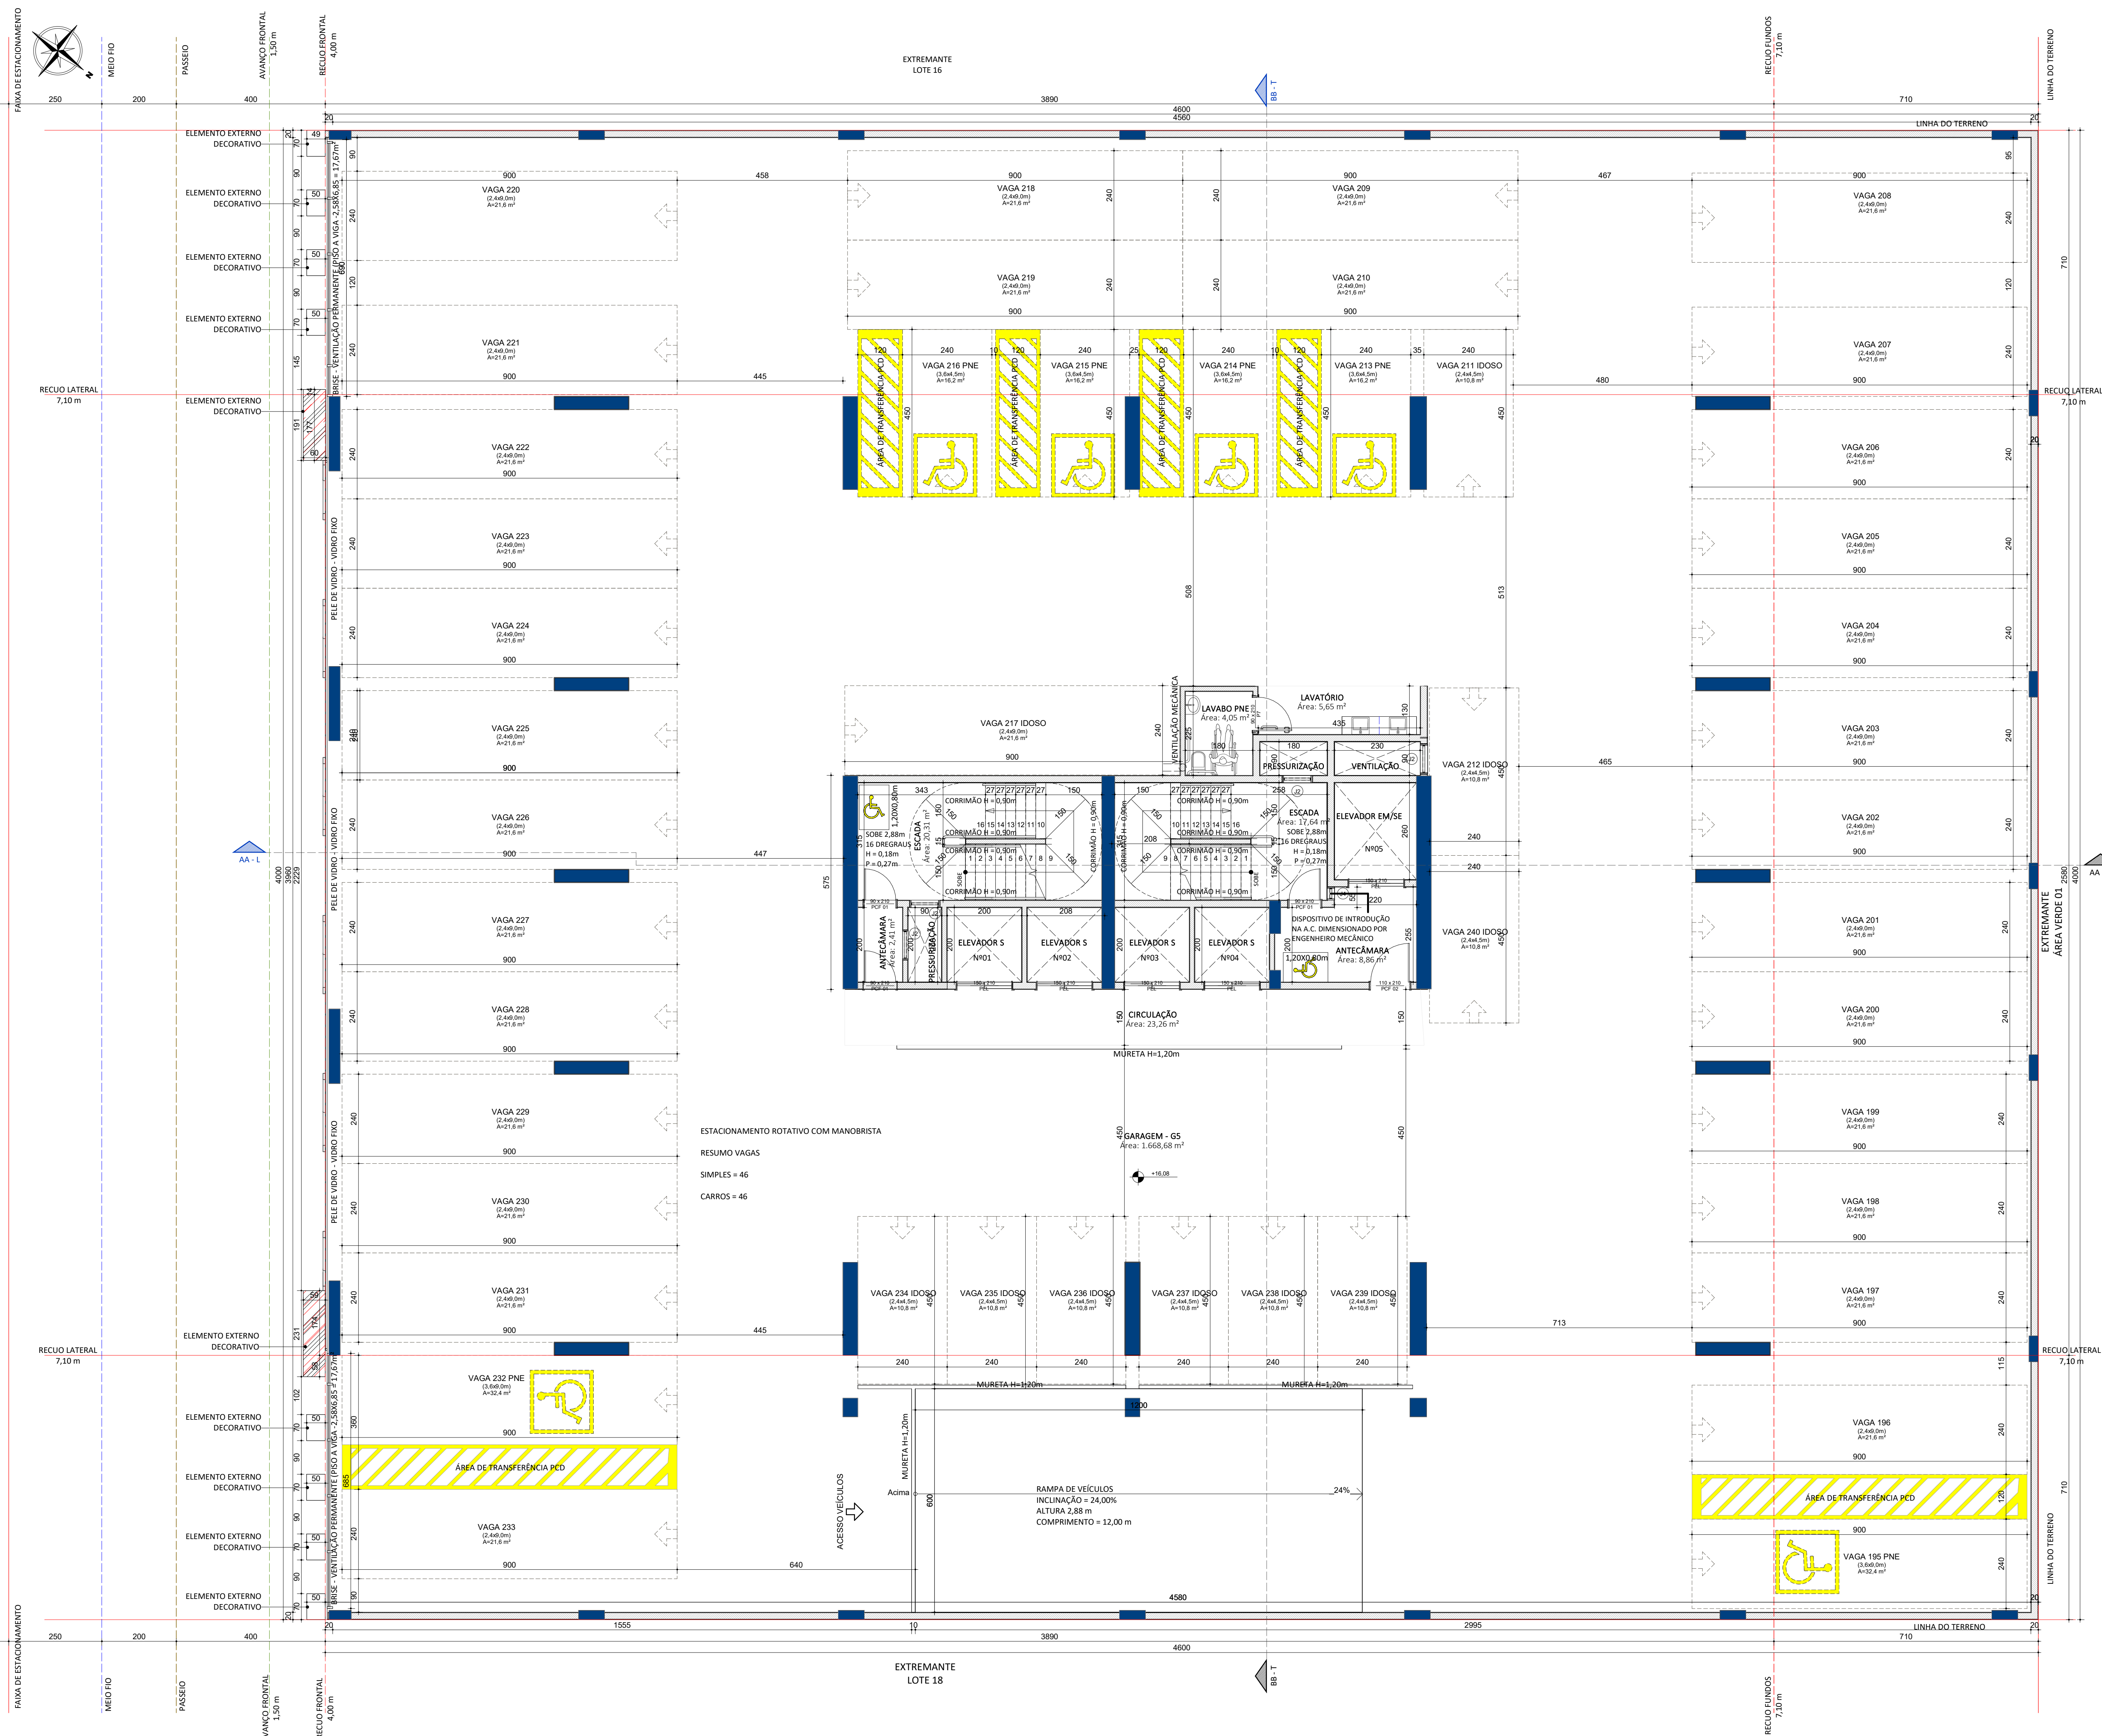


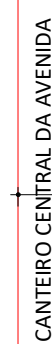

QUADRO DE JANELAS

COD.	QT	COMPRIMENTO	ALTURA	PERÍMETRO	DESCRIÇÃO	ÁREA
13	1	80	50	160	Esquadria de alumínio na cor branco / lãna vidro (Alcoa) Vidro acido	0,4 m ²
14	30	120	120	240	VENEZIANA VENTILADA - 2 FOLHAS - ALUMÍNIO E VIDRO	0,96 m ²
13	51	80	80	160	JANELA MAXIM-AR - 1 FOLHA - ALUMÍNIO E VIDRO	0,64 m ²
14	32	35	120	cerveto	VENEZIANA MAXIM-AR - EMBOREIRO/NOVO EMEC	0,42 m ²
15	2	160	40	120	VENEZIANA VENTILADA - 2 FOLHAS - ALUMÍNIO E VIDRO	0,64 m ²
16	1	150	150	300	JANELA DE DESLIZAR - 2 FOLHAS - ALUMÍNIO E VIDRO	5,8 m ²
104	275	150	120	120	JANELA MAXIM-AR - 1 FOLHA - ALU E VIDRO (ABERTURA)	2,25 m ²

QUADRO DE PORTAS				
COD	QT	COMPRIMENTO	ALTURA	DESCRIÇÃO
A05	1	160	210	PORTA DE ALUMINIO - VISO TEMPLADO
P1	155	90	210	PORTA DE GESSO - FOLHA - MADEIRA
P2	56	80	210	PORTA DE GESSO - FOLHA - MADEIRA
P3	1	210	79	PORTA DE ALUMINIO - VISO TEMPLADO
P4	25	90	210	PORTA DE DESLIZAR - FOLHA - MADEIRA (PNE)
P5	1	90	210	PORTA DE GESSO - FOLHA - VISO - SOB MEDIDA
P6	1	720	250	PORTA DE ALUMINIO - VISO TEMPLADO
P7	8	90	210	PORTA DE ALUMINIO - VISO TEMPLADO
P8	1	300	300	PORTA DE ALUMINIO - VISO TEMPLADO
P9	1	451	300	PORTA DE ALUMINIO - VISO TEMPLADO
P10	1	180	300	PORTA DE ALUMINIO - VISO TEMPLADO
P10	1	500	300	PORTA DE ALUMINIO - VISO TEMPLADO
P11	1	388	300	PORTA DE ALUMINIO - VISO TEMPLADO
P12	1	383	300	PORTA DE ALUMINIO - VISO TEMPLADO
P13	1	200	210	PORTA DE ALUMINIO - VISO TEMPLADO
P14	1	90	210	PORTA DE ALUMINIO - VISO TEMPLADO
P15	1	150	210	PORTA DE ALUMINIO - VISO TEMPLADO
P16	31	150	210	PORTA DE GESSO - FOLHA - CARTA FOGG
P17	158	150	210	PORTA DE GESSO - FOLHA - CARTA FOGG
P18	1	350	300	PORTA DE ALUMINIO - VISO TEMPLADO
P19	1	350	300	PORTA DE ALUMINIO - VISO TEMPLADO
VN2	1	6	150	PORTA VENEZIANA - VISTA
VN2	1	79	210	PORTA VENEZIANA
VN3	3	80	120	PORTA VENEZIANA - VISTA

QUADRO DE VAGAS	
NÍVEL	QTDE
PAV. 01 - TÉRREO	15
PAV. 2 - GARAGEM G1	45
PAV. 3 - GARAGEM G2	45
PAV. 4 - GARAGEM G3	46
PAV. 5 - GARAGEM G4	46
PAV. 6 - GARAGEM G5	46

REVISÃO	ASSUNTO	DESENHO	RESPONSÁVEL	DATA
R1	1º ANÁLISE	GIOVANNI D.	RS CONCEPT	11/11/202



PROJETO

ARQUITETÔNICO

BR

LOTUS BUSINESS CENTER

RUA PROJETADA (AVENIDA RIO PEREQUÊ), Nº 539 - LOTE Nº 16 E LOTE Nº 17
LOTEAMENTO ANDORINHA CENTER, PORTO BELO SC

RESP. TÉCNICO	HÉCTOR RHÁVI DA COSTA CAU: A190987-8	PROPRIETÁRIO L K NOVE EMPREENDIMENTOS IMOBILIÁRIOS SPE LTDA CNPJ 44.023.808/1001-60
---------------	---	--

ATA	OBRA TIPO	BRANCHA
17/05/2024	EDIFÍCIO COMERCIAL E RESIDENCIAL MULTIFAMILIAR	
PROTOCOLO RS 0.2021 LK9	CONTEÚDO PLANTA DO 6º PAVIMENTO GARAGEM - G5 QUADRO DE ESQUADRIAS	7

OBSERVAÇÕES IMPORTANTES:

Escalar que a aprovação do projeto não implica no reconhecimento por parte da Prefeitura do Estado de propriedade do terreno.

Escalar que se informações e os cálculos das áreas constam nesse projeto, são verdadeiras e de inteira responsabilidade do autor do mesmo.

Escalar, em nome do autor do projeto, que está ciente e que foram atendidas as exigências constantes na norma brasileira de edificações habitacionais - ABNT NBR15075.