


CANTIEIRO CENTRAL DA AVENIDA

RUA PROJETADA
AVENIDA RIO PEREQUÊ

CANTIEIRO CENTRAL DA AVENIDA

7º PAVTO - TIPO DIFERENCIADO

ESCALA 1 : 75

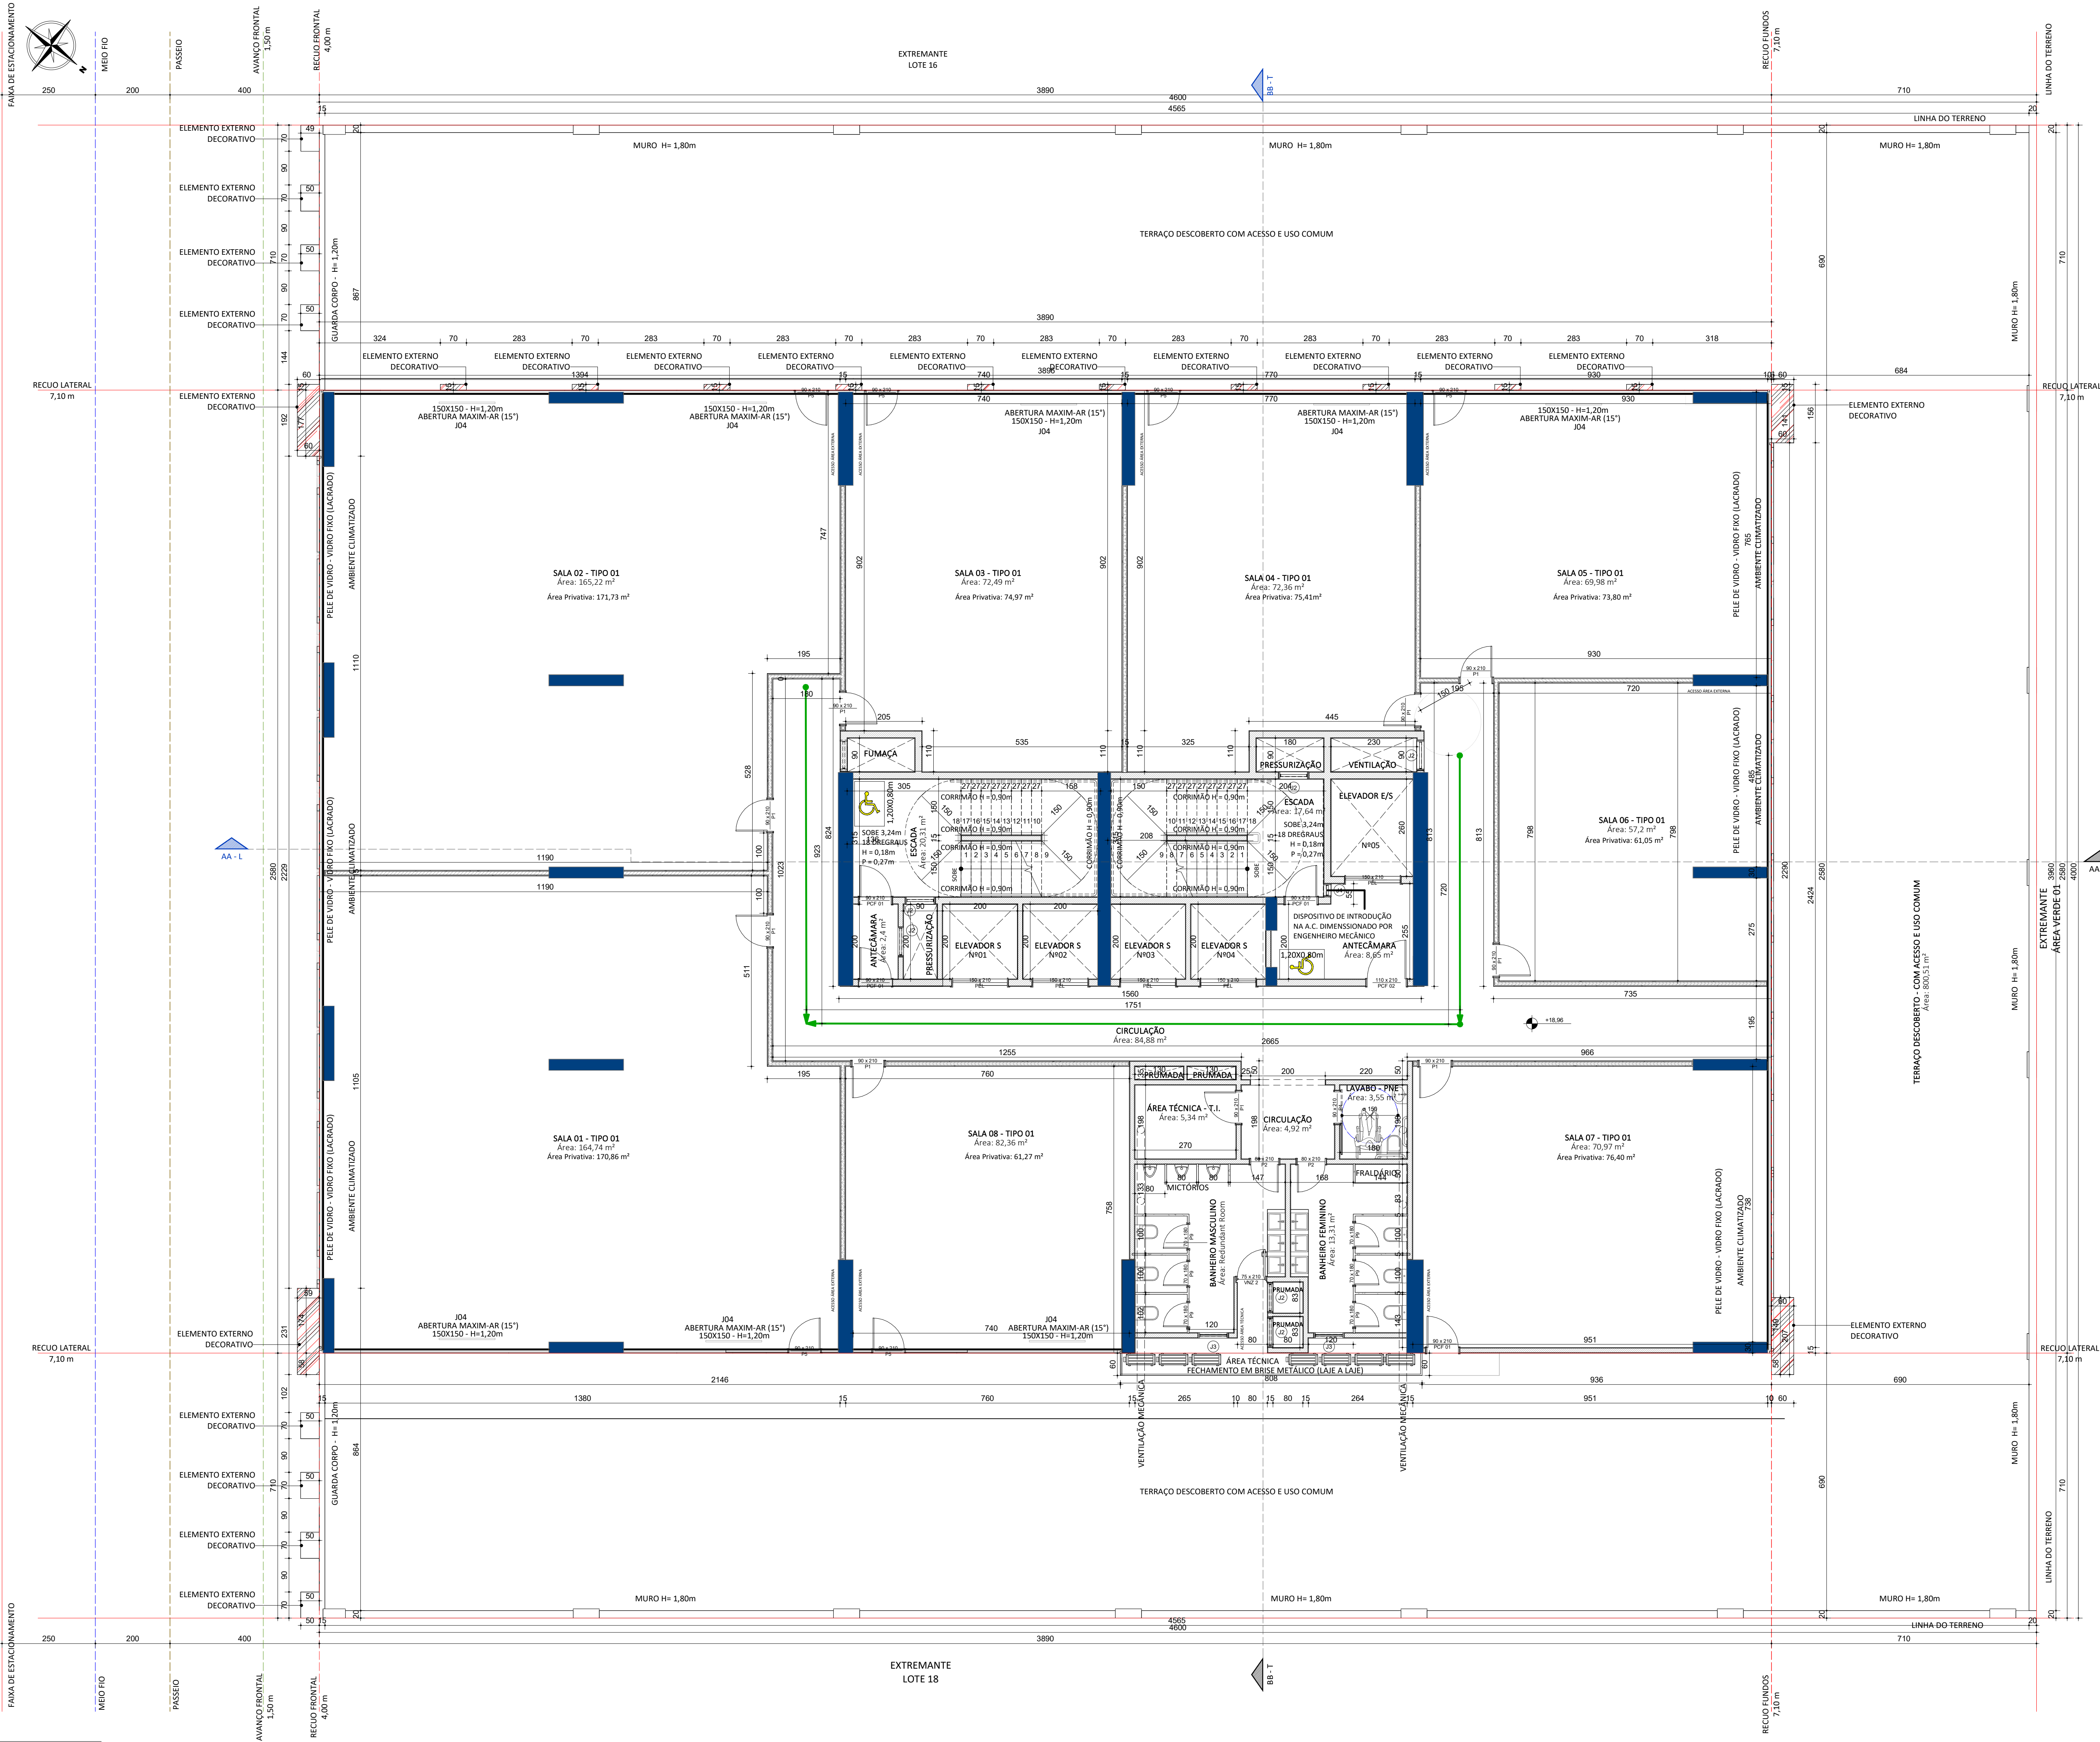

QUADRO DE JANELAS						
CÓD.	QT	COMPRIMENTO	ALTURA	PEITORIL	DESCRIÇÃO	ÁREA
J1	1	80	50	160	Esquadra de alumínio na cor branca / Janela gold (Accon). Vidro acido	0,4 m²
J2	203	80	120	carreiro	VENEZIANA ANTECAMARA	0,96 m²
J3	51	80	80	150	JANELA MAXIM-AR - 1 FOLHA - ALUMÍNIO E VIDRO	0,64 m²
J4	32	80	120	carreiro	VENEZIANA ANTECAMARA - DIMENSIONADA ENG MEC	0,64 m²
J5	2	160	40	150	VENEZIANA VENTILADA	0,64 m²
J6	1	150	120	120	JANELA DE DESLIZAR - 2 FOLHAS - ALUMÍNIO E VIDRO	1,8 m²
J9	295					
J04	271	150	150	120	JANELA MAXIM-AR - 1 FOLHA - ALU E VIDRO (ABERTURA 150x150)	2,25 m²

QUADRO DE PORTAS				
CÓD	QT	COMPRIMENTO	ALTURA	DESCRIÇÃO
A25	6	160	210	Porta Doble Interior de Gfro
P1	155	90	210	PORTA DE GIRO - 1 FOLHA - MADEIRA
P2	56	80	210	PORTA DE GIRO - 1 FOLHA - MADEIRA
P3	1	70	210	PORTA DE GIRO - 1 FOLHA - MADEIRA
P4	25	80	210	PORTA DE GIRO - 1 FOLHA - MADEIRA (PNE)
P5	6	90	210	PORTA DE GIRO - 1 FOLHA - VIDRO - SOB MEDIDA
P6	1	720	210	PORTA DE ABIR - 1 FOLHA - MADEIRA (PNE)
P7	8	90	210	PORTA AUTOMÁTICA - VIDRO TEMPERADO
P8	2	300	300	PORTA AUTOMÁTICA - VIDRO TEMPERADO
P9	1	411	300	PORTA DE GIRO - 1 FOLHA - SANTÁRIOS
P10	1	500	300	PORTA GARAGEM
P11	1	100	300	PORTA DE VIDRO - SOB MEDIDA
P12	1	383	300	PORTA DE VIDRO - SOB MEDIDA
PC01	1	200	210	PORTA 1 FOLHA - ALUMÍNIO COM BARRA ANTI-PANICO
PC1 01	94	90	210	PORTA DE GIRO - 1 FOLHA - CORTA FOSDO
PC1 02	35	110	210	PORTA DE GIRO - 1 FOLHA - CORTA FOSDO
PS	158	150	210	PORTA DO ELEVADOR
PD01	1	350	300	PORTA GARAGEM
VNZ 1	6	130	210	PORTA VENEZIANA
VNZ 2	35	75	210	PORTA VENEZIANA
VNZ 3	742	89	120	PORTA VENEZIANA - VISTA

REVISÃO	ASSUNTO	DESENHO	RESPONSÁVEL	DATA
R1	1º ANÁLISE	GIOVANNI D.	RS CONCEPT	11/11/2024



PROJETO

OBRA

RESP. TÉCNICO

PROPRIETÁRIO

ARQUITETÔNICO

LOTUS BUSINESS CENTER

RUA PROJETADA (AVENIDA RIO PEREQUÊ), Nº 539 - LOTE Nº 16 E LOTE Nº 17

LOTEAMENTO ANDORINHA CENTER, PORTO BELO SC

HÉCTOR RHAVI DA COSTA

CAU: A190987-8

L K NOVE EMPREENDIMENTOS IMOBILIÁRIOS SPE LTDA

CNPJ 44.023.808/1001-60

DATA: 17/05/2024

PROTOCOLO RS 70.2021.LK9

OBRA TIPO: EDIFÍCIO COMERCIAL E RESIDENCIAL MULTIFAMILIAR

CONTEÚDO: PLANTA DO 7º PAVIMENTO TIPO DIFERENCIADO (X1)

QUADRO DE ESQUADRIAS

ESCALA INDICADA

OPERAÇÕES IMPORTANTES:

1. Declaram que a aprovação do projeto não implica no reconhecimento por parte da Prefeitura de Belo Horizonte do conteúdo do projeto.

2. Declaram que as informações e os cálculos das áreas contidas nesse projeto, são verdadeiras e de sua responsabilidade de acordo com o projeto.

3. Declaram, como parte do projeto, que estão cientes e que assumem a responsabilidade de qualquer alteração no projeto realizada em decorrência de alterações técnicas.

4. Declaram, como parte do projeto, que estão cientes e que assumem a responsabilidade de qualquer alteração no projeto realizada em decorrência de alterações técnicas.

5. Declaram, como parte do projeto, que estão cientes e que assumem a responsabilidade de qualquer alteração no projeto realizada em decorrência de alterações técnicas.